

INDICADORES URBANOS

USO	EDIFICAÇÃO DE USO RESIDENCIAL UNIFAMILIAR	
PROPOSTO		
TAXA DE PERMEABILIDADE	46,26%	
TAXA DE OCUPAÇÃO	53,74%	
ÍNDICE DE APROVEITAMENTO	0,53	
ALTURA MÁXIMA DA EDIFICAÇÃO – COBERTO	7,80m	
TESTADA MÍNIMA	10,00m	
RECUIO DE FRENTE	4,75m	
RECUIO DE FUNDO	2,90m	
RECUIO DE LATERAL	1,50m	
ÁREA DO LOTE	270,00m²	

QUADRO GERAL DE ÁREAS

ÁREA DO TERRENO	270,00m²
ÁREA CONSTRUIDA PAV. TERREO	145,11m²
ÁREA CONSTRUIDA PAV. SUPERIOR	139,20m²
ÁREA DE COBERTURA	158,42m²
ÁREA PERMEÁVEL	98,89m²
ÁREA OCUPADA	76,11m²

QUADRO DE ESQUADRIAS

COD	LARG.	ALTURA	PERÍMETRO	QUANT.	OBSERVAÇÕES
P01	1,00	2,10	-	01	PORTÃO EM ALUMÍNIO BRANCO (CORRER)
P12	3,60	2,50	-	01	PORTÃO EM ALUMÍNIO BRANCO (CORRER)
P13	0,90	2,10	-	01	PORTÃO EM GRADE DE FERRO (ABRIR)
P01	1,50	2,10	-	02	PORTA PIVOTANTE EM MADEIRA MACIÇA (ABRIR)
P02	1,00	2,10	-	02	PORTA EM MADEIRA MACIÇA (ABRIR)
P03	0,80	2,10	-	07	PORTA EM MADEIRA MACIÇA (ABRIR)
P04	0,70	2,10	-	07	PORTA EM MADEIRA MACIÇA TODA VENEZ. (ABRIR)
J01	2,00	1,10	1,00	03	JANELA EM VÍDRO TEMPERADO 8mm (CORRER)
J02	1,20	1,10	1,00	01	JANELA EM VÍDRO TEMPERADO 8mm (CORRER)
J03	0,60	0,60	1,50	05	JANELA EM VÍDRO TEMPERADO 8mm (CORRER)
J04	0,40	1,10	1,00	02	JANELA VÍDRO PIVOTANTE EM VÍDRO TEMPERADO 8mm
J05	2,00	1,10	1,00	02	GRADE DE FERRO

QUADRO DE ESQUADRIAS

APROVAÇÕES


TÍTULO:	PROJETO EDIFICAÇÃO UNIFAMILIAR
PROJETO:	EXECUTIVO - ARQUITETÔNICO
ENGENHEIRO:	RUA CORONEL BENTO ALVES, FAZENDINHA, SN, ITAIPICA-CE
PROPRIETÁRIO:	
AUTOR DO PROJETO:	JOSÉ EDUCARIO BRAGA
RESPONSÁVEL TÉCNICO:	ENGENHEIRO CIVIL - RODOLFO GONÇALVES SANTOS CREA CE: 0818107002

CONTEÚDO:	ENGENHEIRO CIVIL - RODOLFO GONÇALVES SANTOS CREA CE: 0818107002
-----------	--


CONTEÚDO:	PLANTA BAIXA TERREO PLANTA BAIXA SUPERIOR QUADRO DE ÁREAS QUADRO DE ESQUADRIAS
-----------	---

DATA:	ABRIL/2019	ESCALA:	INDICADA	DESENHO:	PRANCHETA:
					112


OBS: 1 - OS DESENHOS AUTÓGRAFOS DESTE PROJETO SÃO RESERVAÇÃO PARA ELA, NÃO DEVENDO SER REPRODUZIDOS SEM A AUTUA E ASSINATURA DO ENGENHEIRO RESPONSÁVEL TÉCNICO. 2 - CADERNÃO DEBENTER DO PROJETO NÃO ESTÁ SENDO ENTREGUE, POR NÃO SER DE RESPONSABILIDADE DO PROFISSIONAL INDICADO.

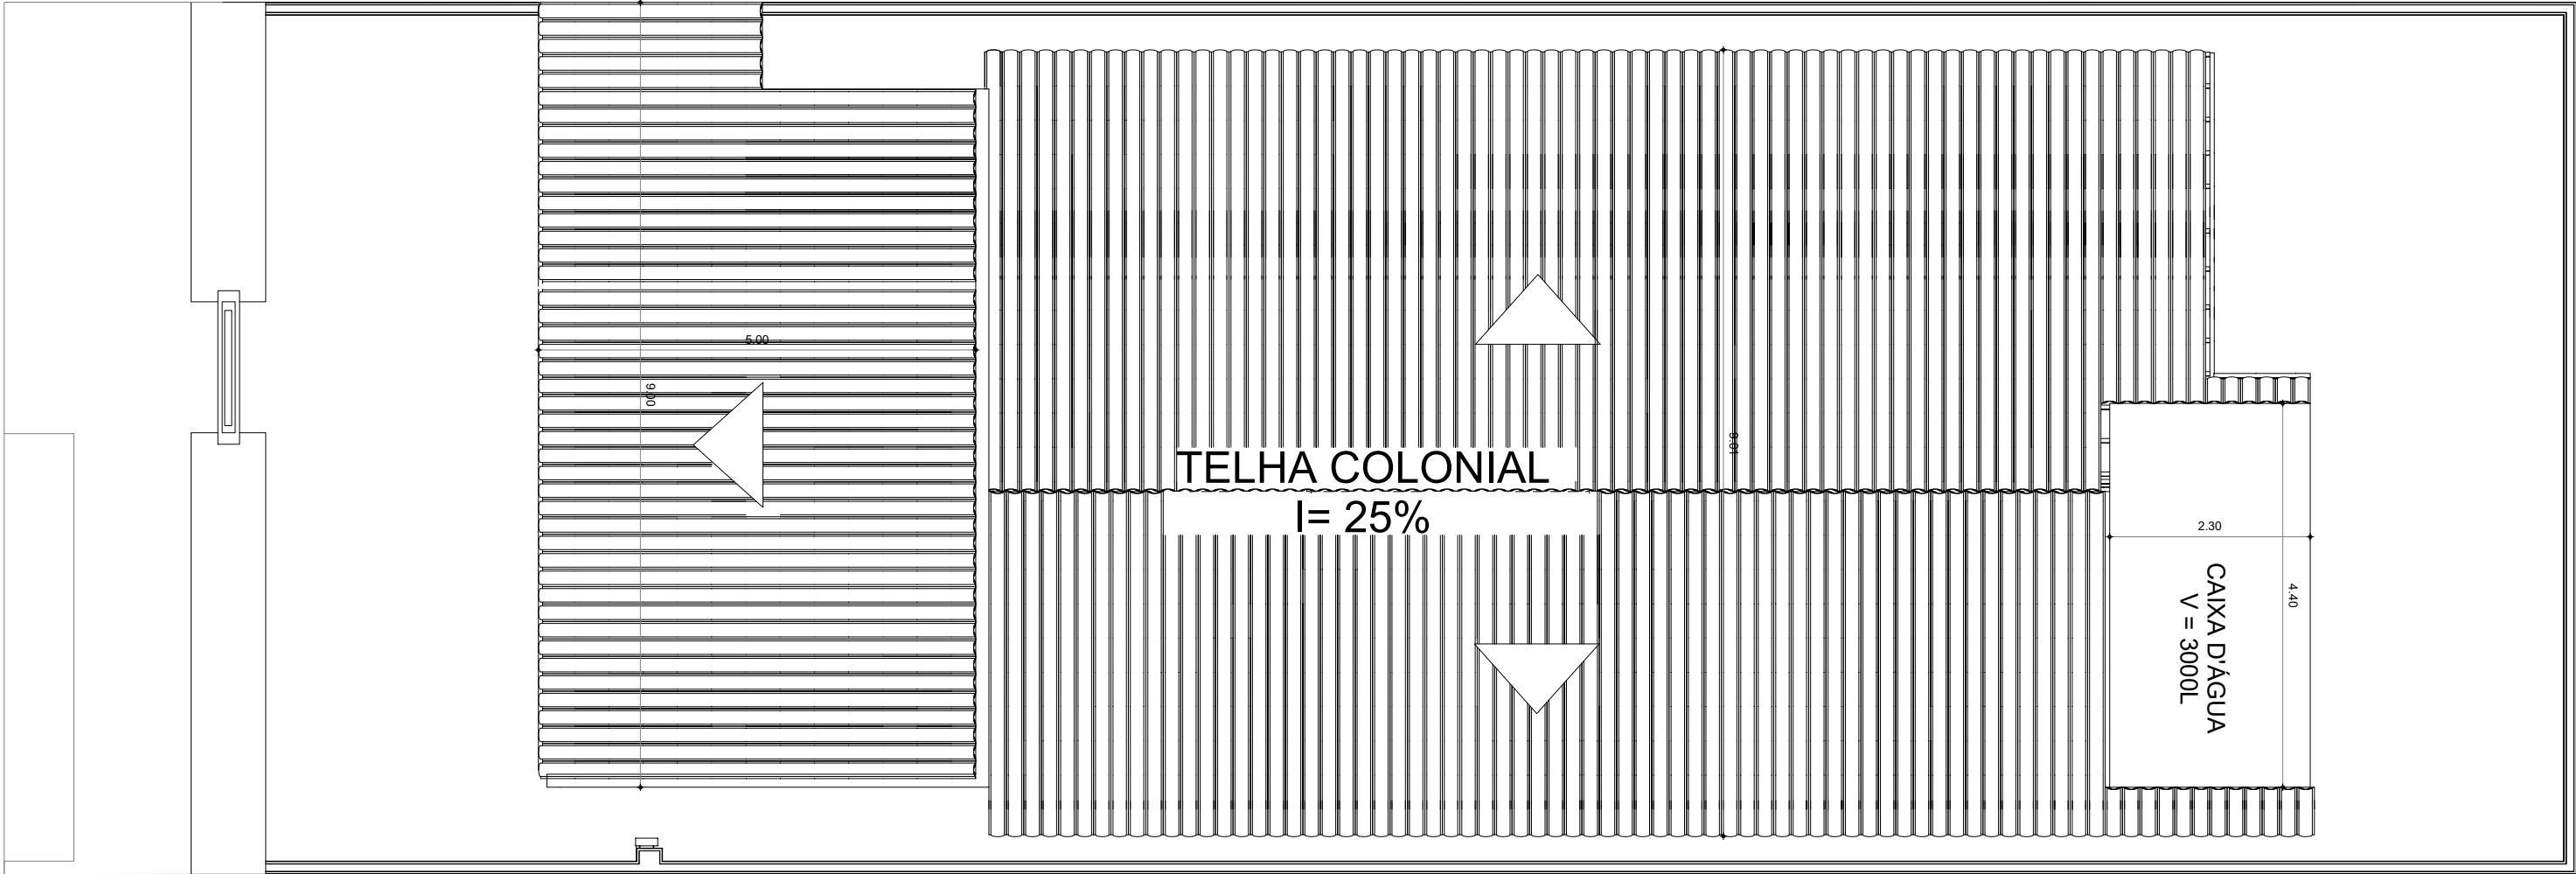

03 PLANTA DE COBERTA
ESCALA — 1 : 75

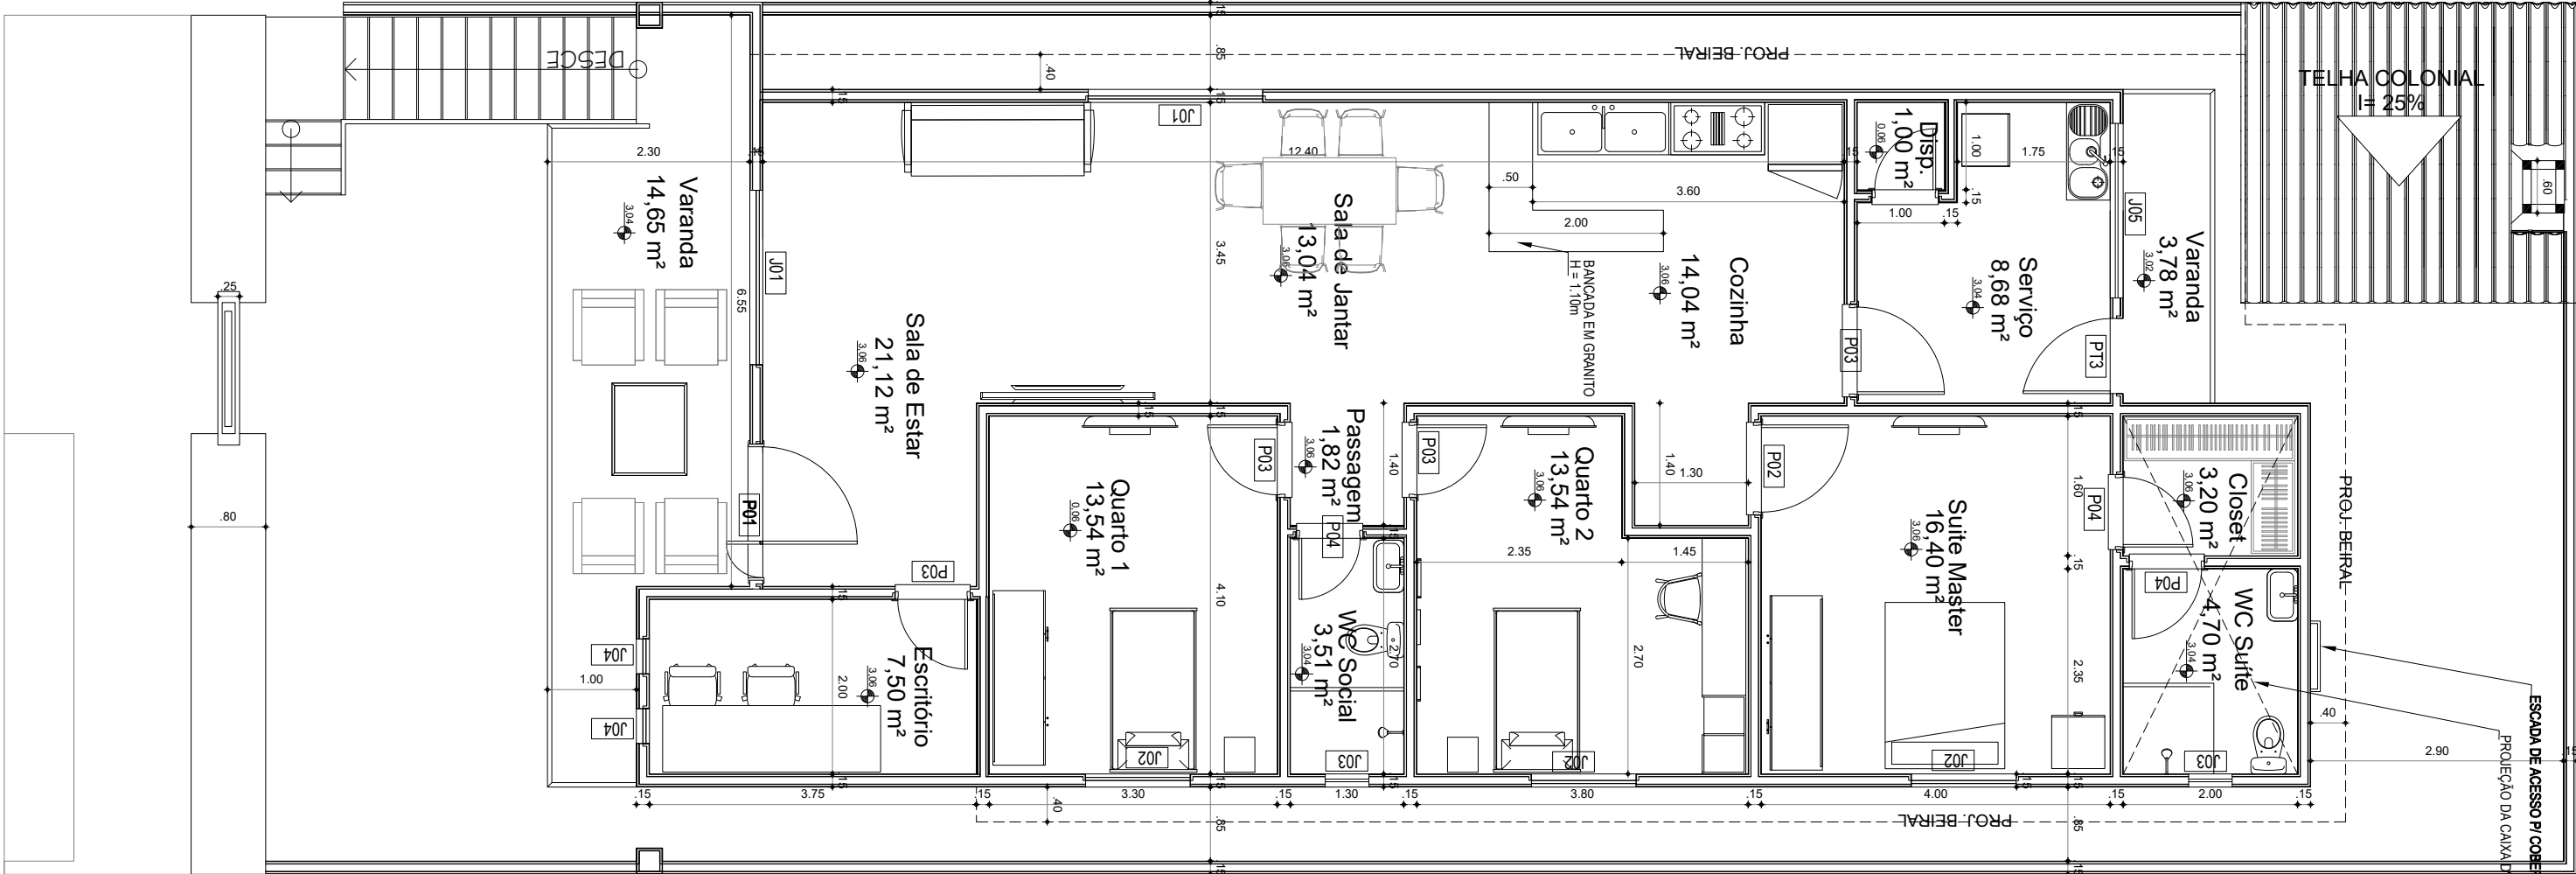

02 PLANTA BAIXA SUPERIOR
ESCALA — 1 : 75

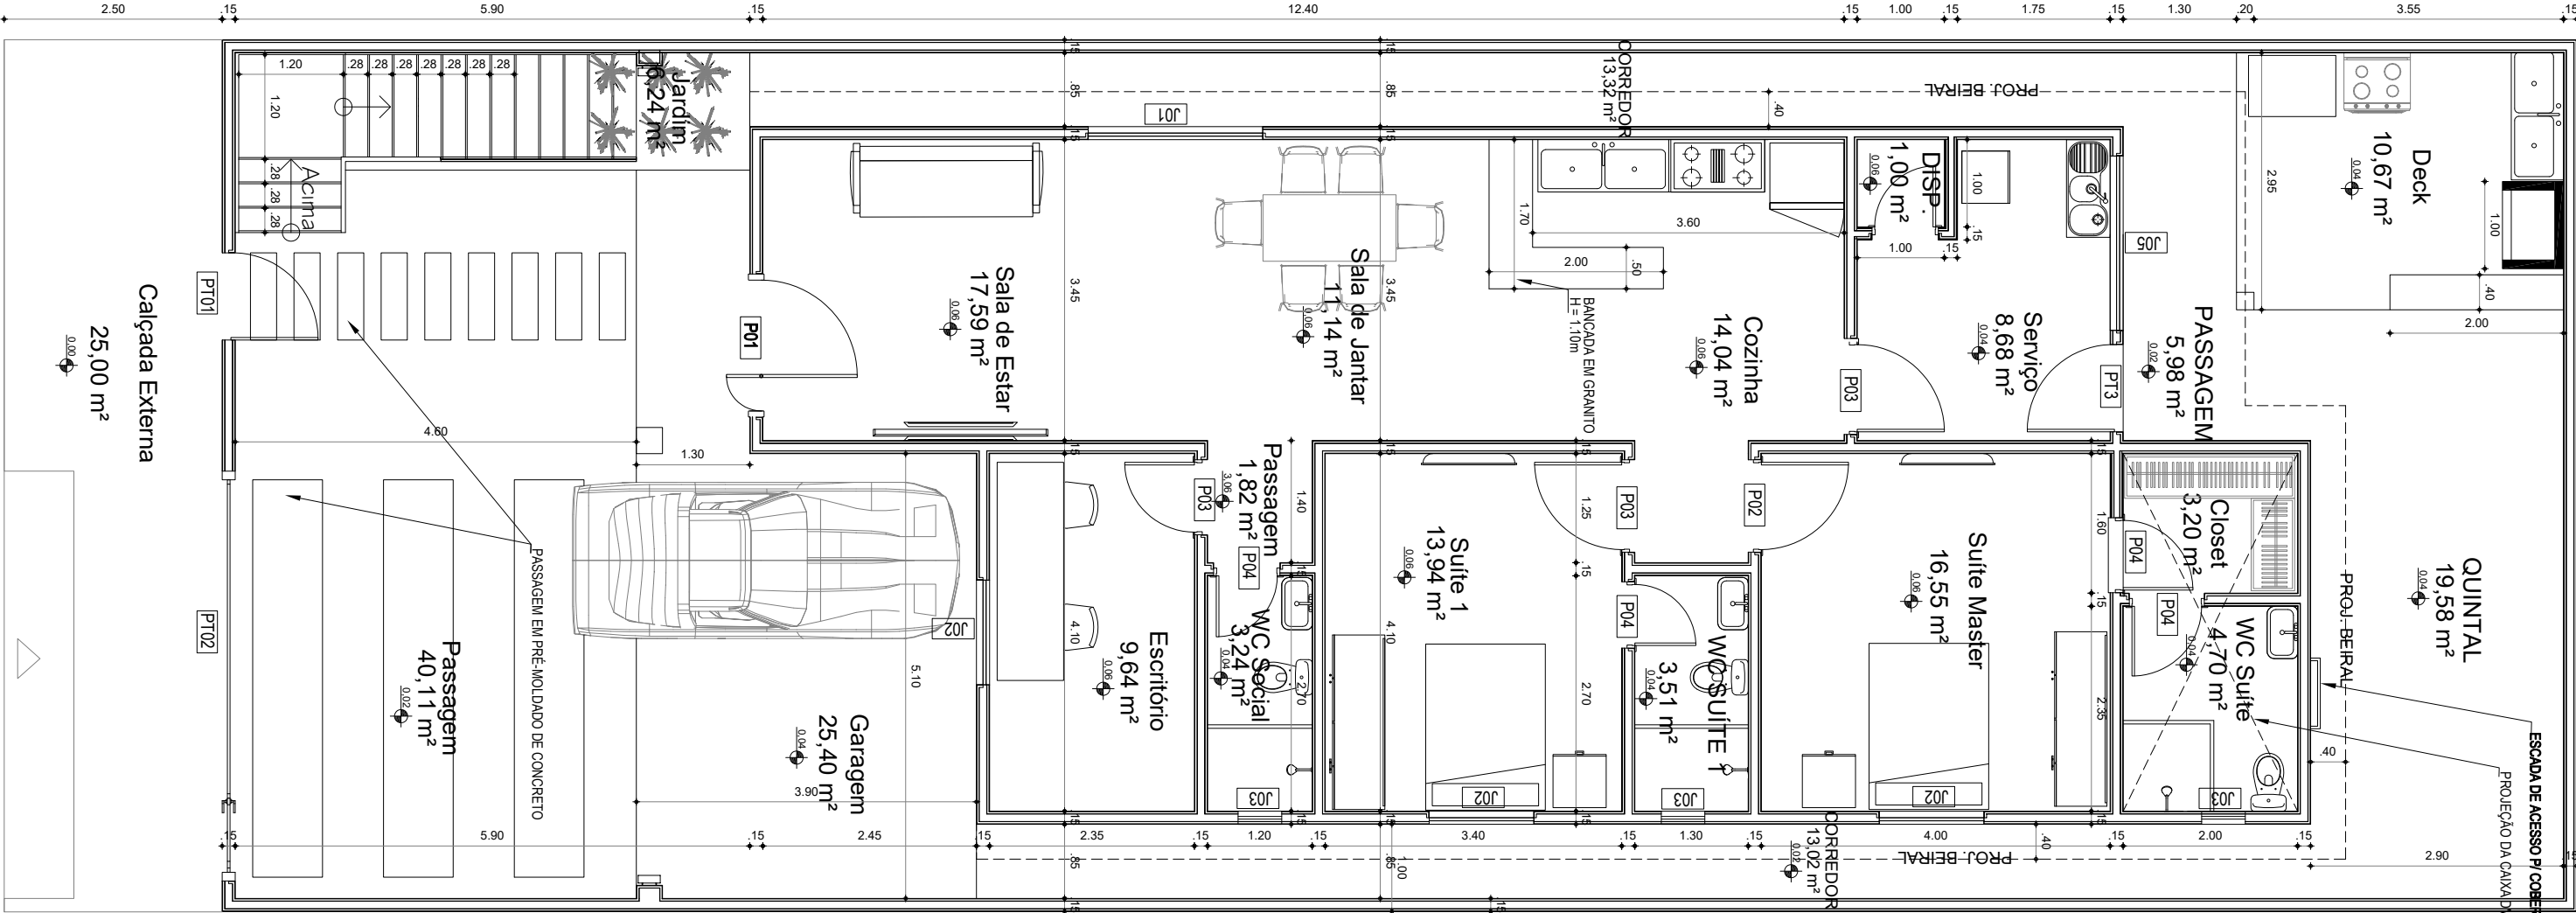

01 PLANTA BAIXA TERREO
ESCALA — 1 : 75