

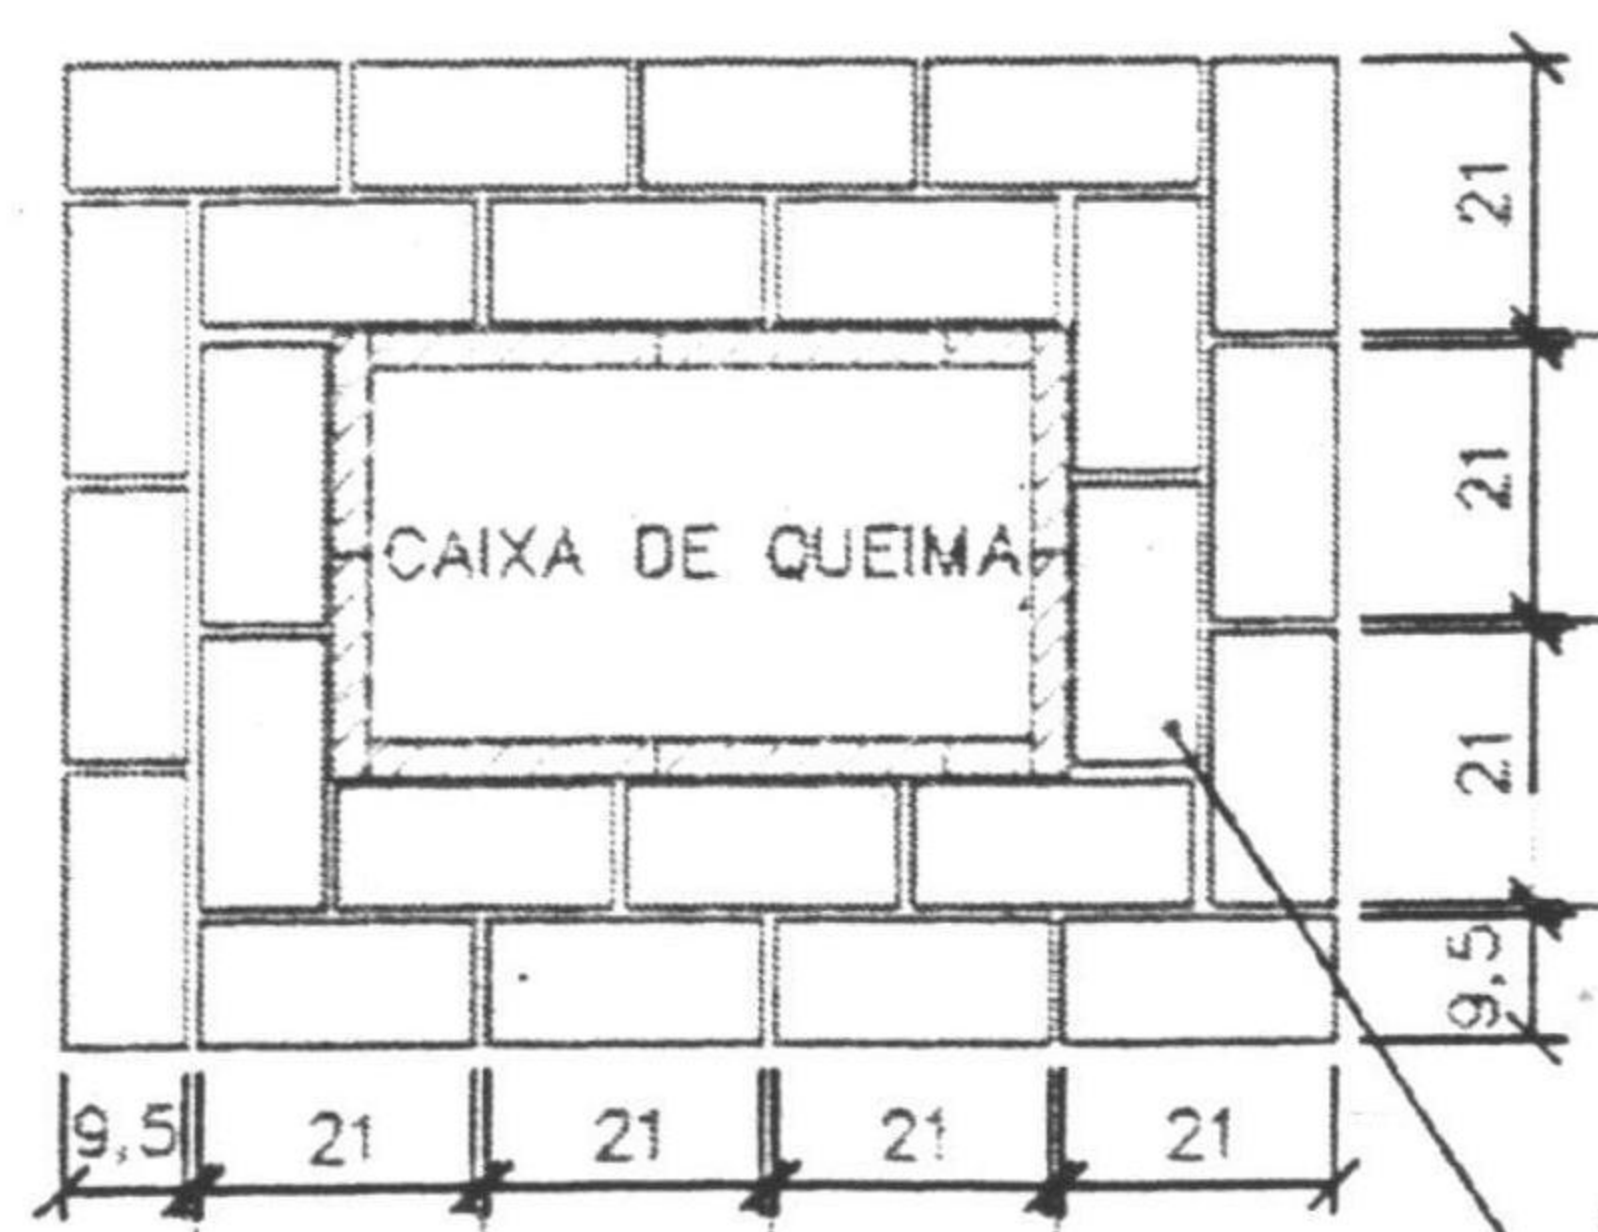


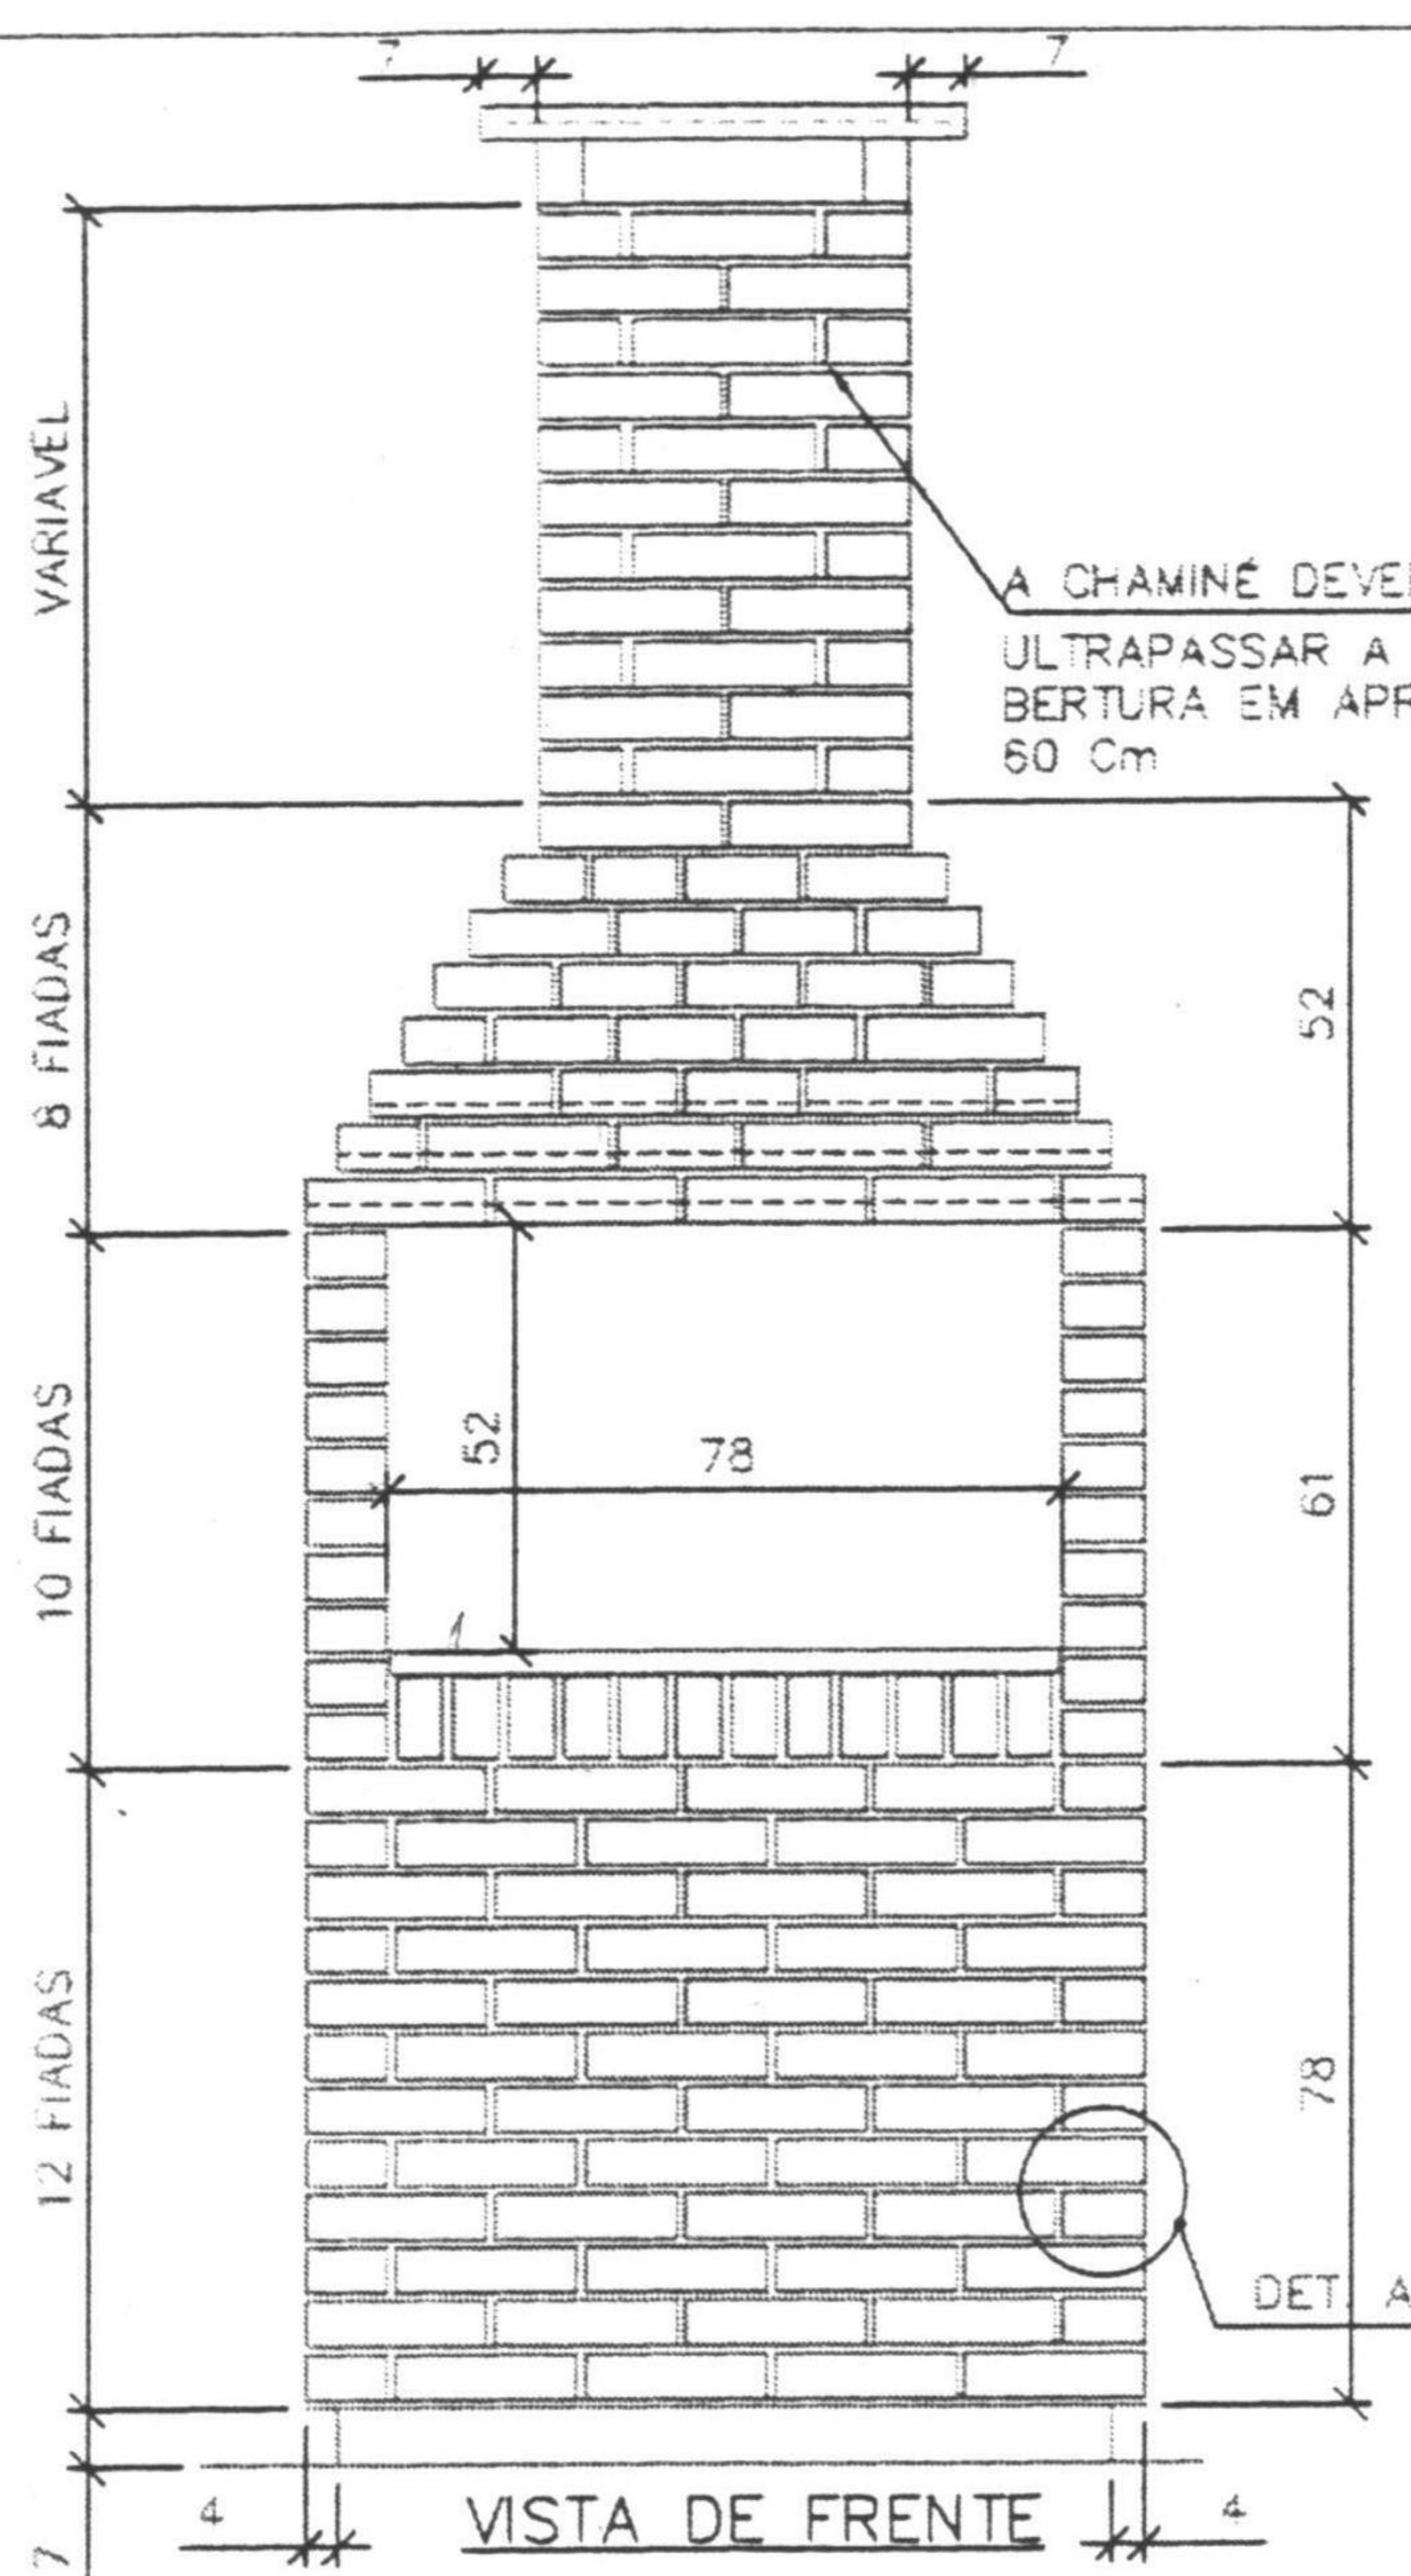

TIPO 1 - PLANTA
UTILIZAR TIJOLOS 21x9,5x5

OS TIJOLOS DA FIADA INTERNA SERÃO
ASSENTADOS EM PÉ (LADO MAIS ESTREITO)

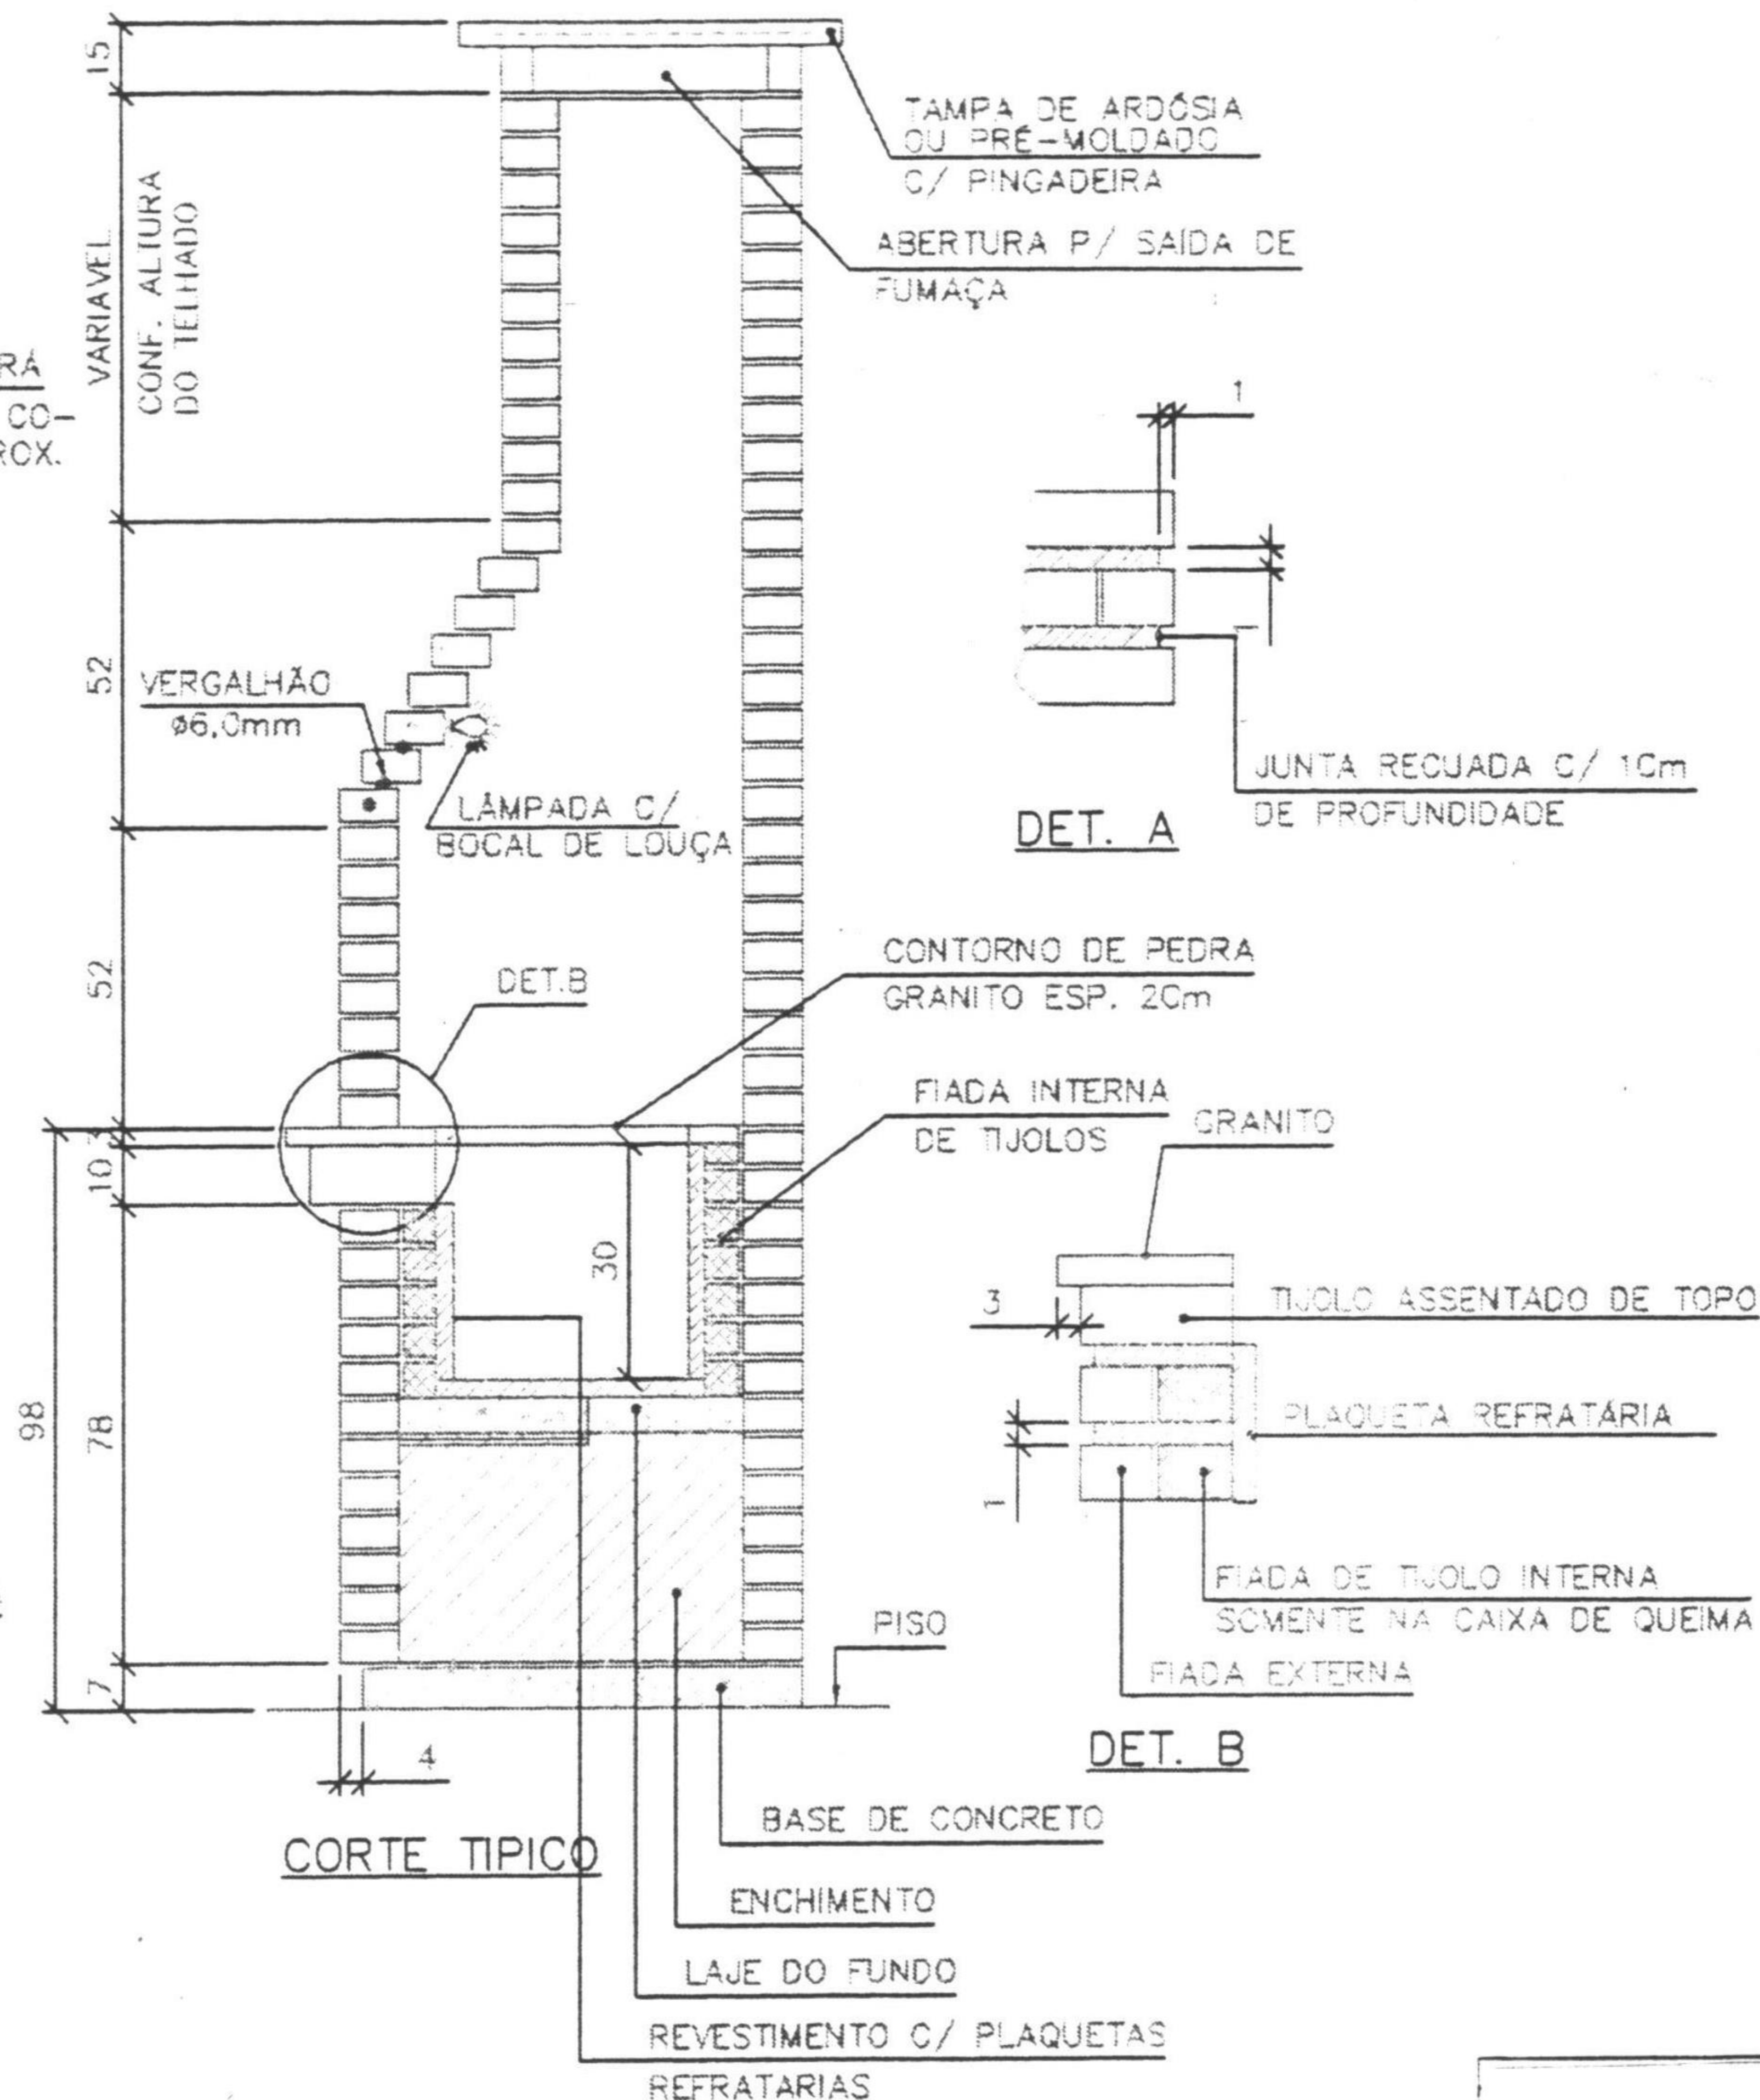

NOTAS:

- 1 - ASSENTAR OS TIJOLOS NIVELADOS E APRUMADOS.
- 2 - MONTAR AS JUNTAS DE 1 x 1 cm.
- 3 - ASSENTAR OS TIJOLOS C/ ARGAMASSA DE CIMENTO, AREIA E CAL-TRAÇO: 1:3:2
- 4 - DURANTE O ASSENTAMENTO DOS TIJOLOS, NÃO DEIXAR RESÍDUOS DE ARGAMASSA NA SUPERFÍCIE EXTERNA EVITANDO O BRANQUEAMENTO DOS MESMOS.
- 5 - A BASE DA CHURRASQUEIRA DEVERÁ SER RECUADA.
- 6 - DIMENSÕES EM CENTÍMETROS.
- 7 - FAZER O PRÉ-AQUECIMENTO, ANTES DE UTILIZAR A CHURRASQUEIRA C/ CARGA TOTAL.
- 8 - INSTALAR VERGALHÃO Ø 6,0mm NAS 3 (TREIS) PRIMEIRAS FIADAS INTERNAMENTE NO TIJOLO OU ENTRE FIADAS EVITANDO TRINCAS.
- 9 - VIDE DETALHES ILUSTRATIVOS DE CONSTRUÇÃO (A) E (B)
- 10 - CONSIDERAR MEDIDAS E NÃO N° DE FIADAS QUE SÃO ORIENTATIVAS E VARIÁVEIS CONFORME TIPO DO TIJOLO.
- 11 - PARA EQUIPAMENTO (CHURRASQUEIRA) GIRATÓRIA CONSIDERAR AS DIMENSÕES DO FABRICANTE.
- 12 - PROCEDER A LIMPEZA C/ SOLUÇÃO DE ÁCIDO MURIÁTICO OU CLORO E ÁGUA A 50%. APÓS 24 HORAS APLICAR 1(UMA) DEMÃO DE IMPERMEABILIZANTE OU HIDROFUGANTE.