



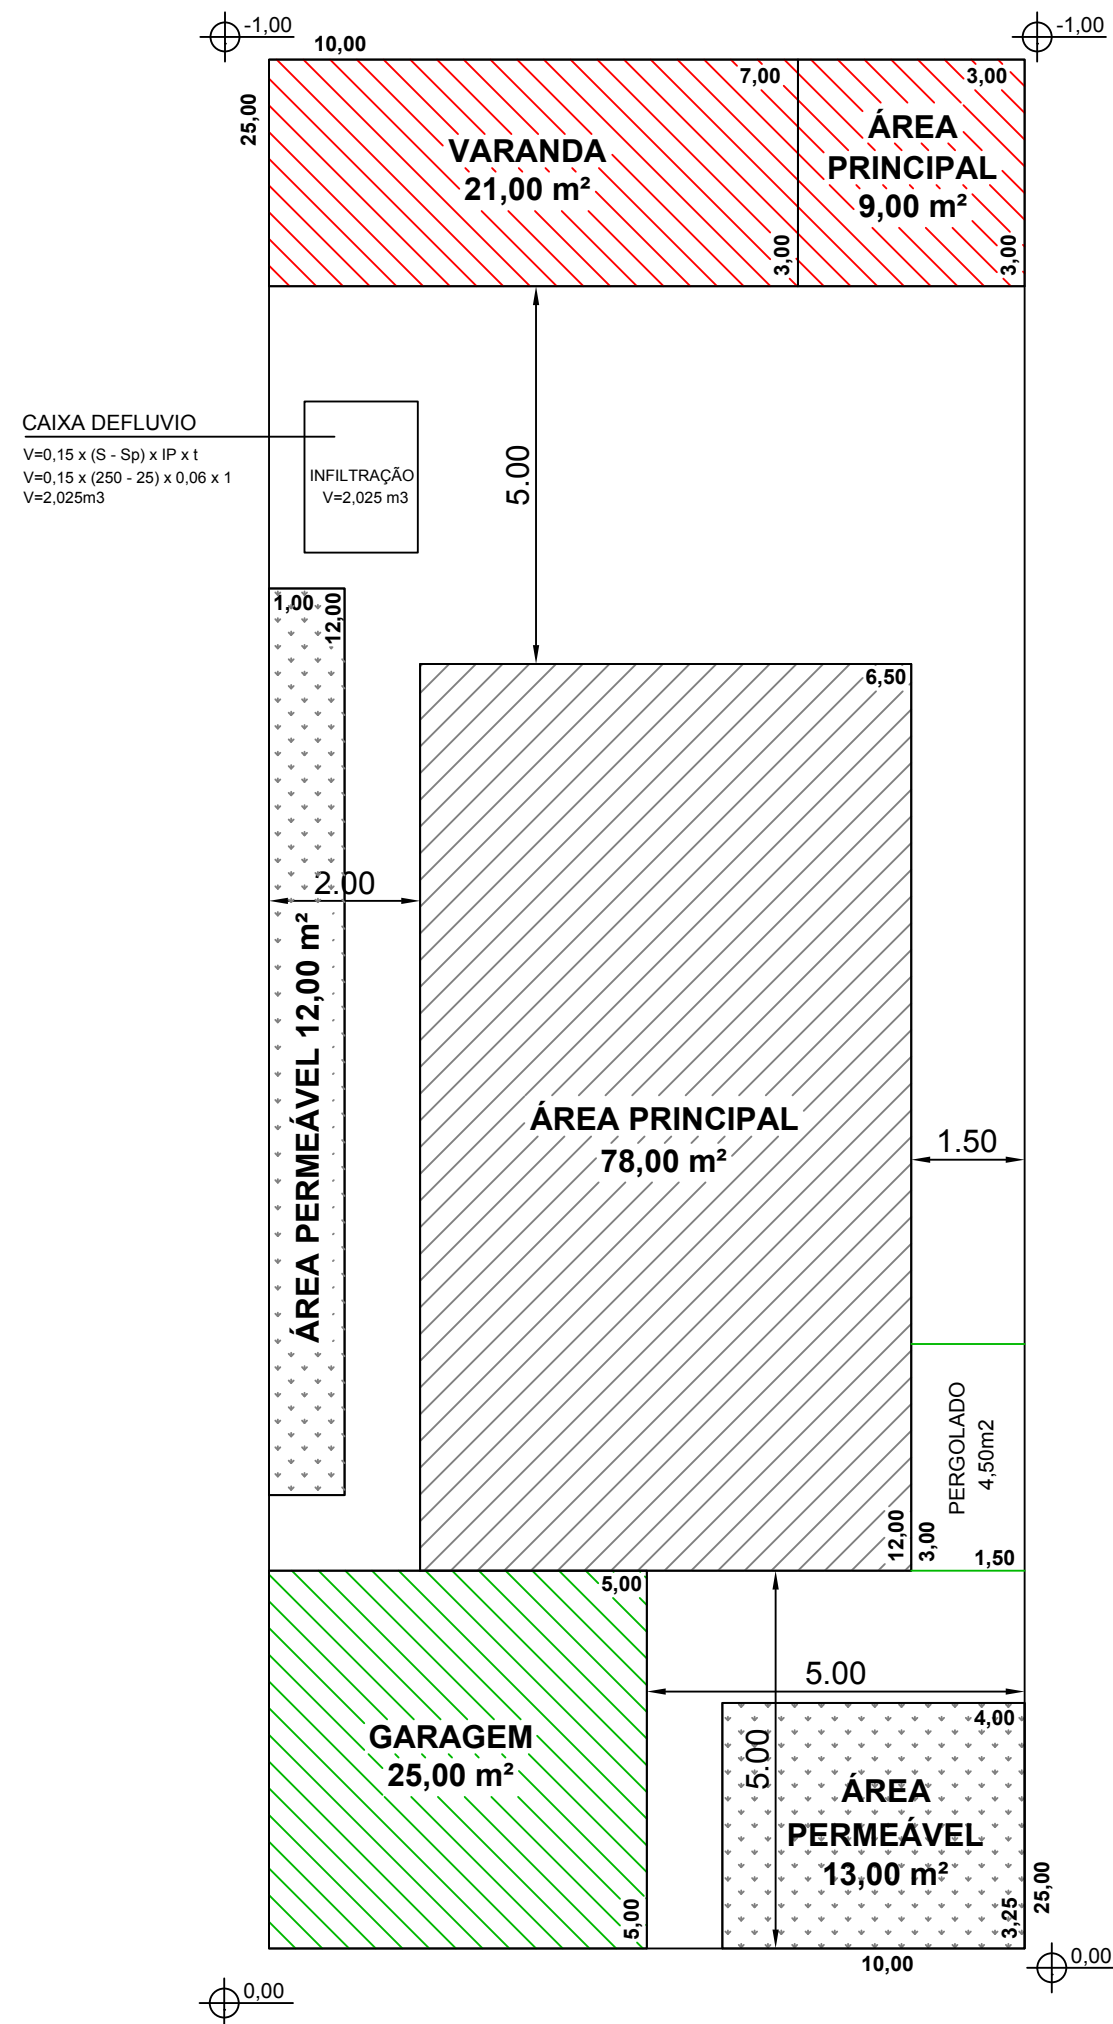

PAV. TERREO
Escala 1:100

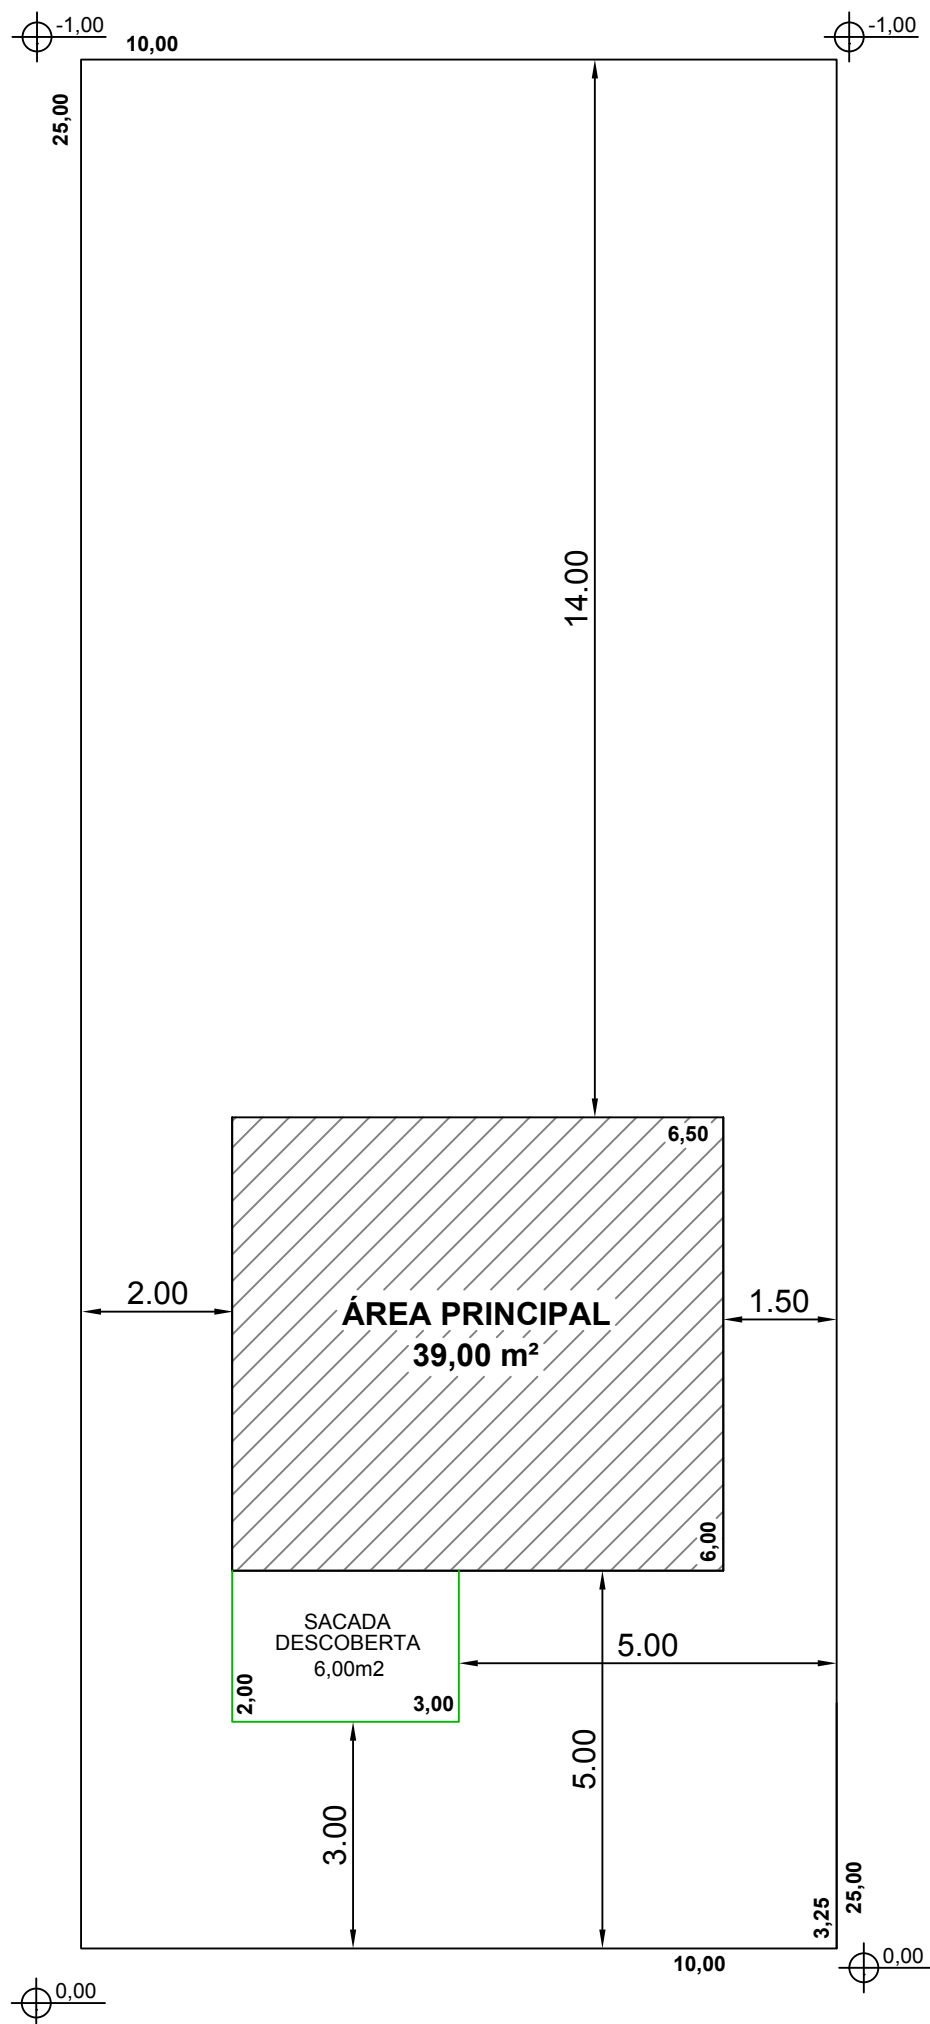

PAV. SUPERIOR
Escala 1:100

LEGENDA


CONSTRUÇÕES

- ÁREA EXISTENTE
- ÁREA À REGULARIZAR/LEGALIZAR
- ÁREA À CONSTRUIR/CONSTRUÇÃO
- ÁREA À DEMOLIR
- OBRAS COMPLEMENTARES

ÁREAS PERMEÁVEIS

- ÁREA PERMEÁVEL - SOLO NATURAL
- PISO PERMEÁVEL

CORTE ESQUEMATICO Escala 1:100

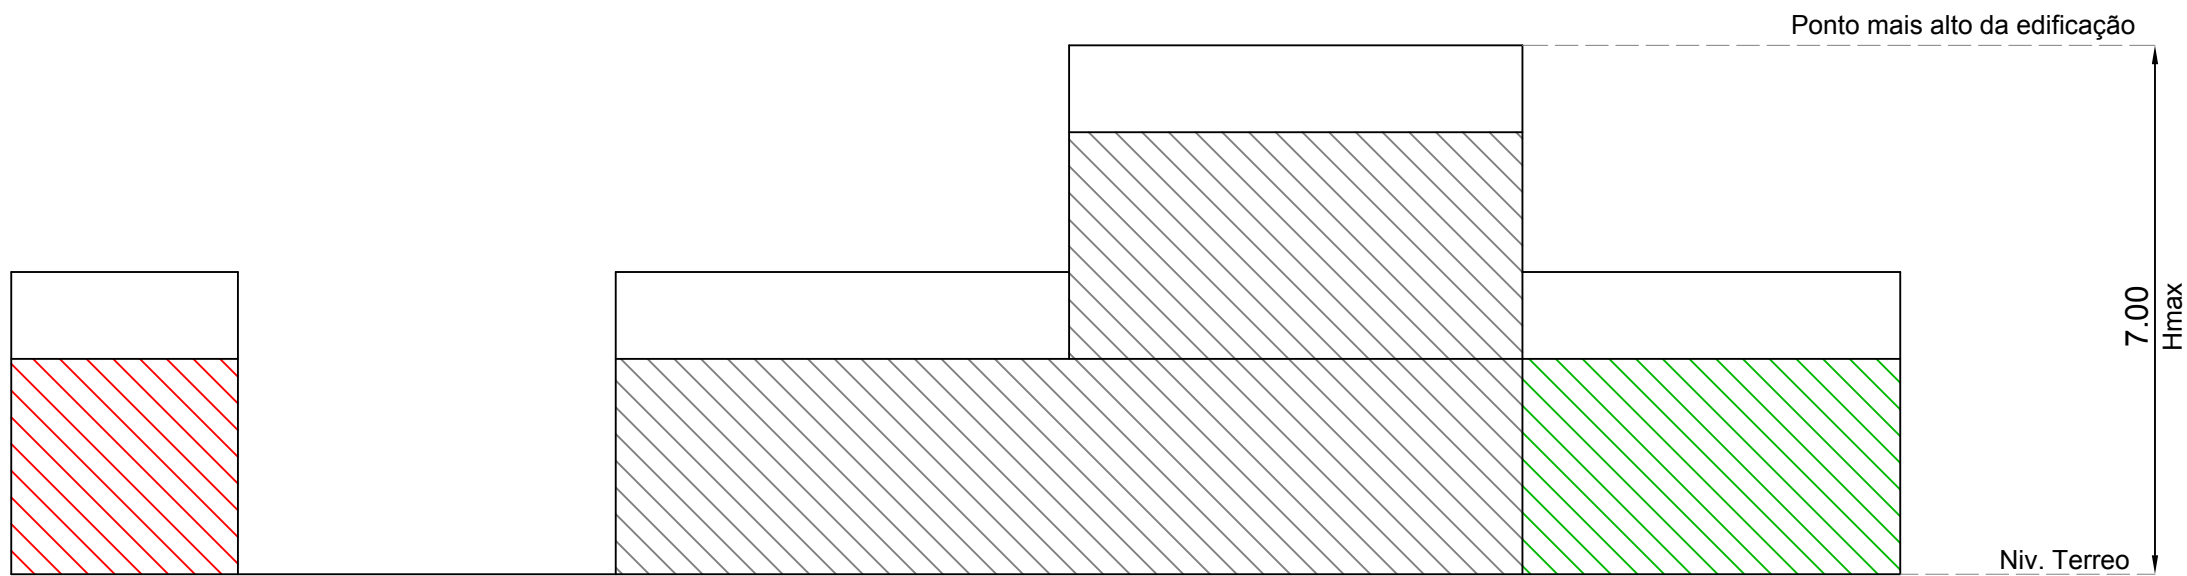

DECLARAÇÕES - 2019	
1	LEGISLAÇÃO: Os responsáveis técnicos declaram o pleno conhecimento da legislação municipal vigente, a saber, as Leis Complementares 2932 de 10 de Janeiro de 2019 (Código de Obras Municipais) e 2157/2007 (Lei de Parcelamento, Uso e Ocupação do Solo) e demais leis que regulamentam construções como o Decreto Estadual de Segurança Contra Incêndios das edificações e a Lei de Risco no Estado de São Paulo, as Leis e Decretos de licenciamento e ambientais, Plano de Proteção de Voo (COMAER), regulamentação da Vigilância Sanitária, Normas Regulamentadoras do Ministério do Trabalho, entre outros.
2	PROJETO SIMPLIFICADO e ANÁLISE SIMPLIFICADA: Com base na LC 2932/2019, Artigos 12 a 14, Decreto 028/2019 - Institui e regulamenta Projeto Simplificado para aprovação de edificações residenciais e não residenciais e no Decreto 272/19 - Institui o procedimento de análise simplificada, aprovação de projeto e concessão de Alvará de Construção neste município, para edificações residenciais e não residenciais de todos os portes, tanto para procedimentos eletrônicos como físicos (impresos), serão realizadas análises e simplificações apenas sobre os itens especificados nas legislações e decretos citados.
3	REGULARIZAÇÃO OU LEGALIZAÇÃO: Quando se tratar de projeto de Regularização ou Legalização, havendo ou não reforma, reparo, intervenções estruturais, os responsáveis técnicos, declaram mediante a assinatura deste projeto que não foram encontradas irregularidades que comprometam a estrutura da obra e que o imóvel tem condições de habitabilidade, não oferecendo qualquer tipo de risco aos seus usuários.
4	DIVERGÊNCIA ENTRE PROPRIETÁRIO E RESPONSÁVEIS TÉCNICOS: Quaisquer divergências entre o Responsável Técnico pela Elaboração do Projeto, pelo Execução da Obra e Proprietário, deverão ser tratadas e eliminadas no âmbito da Justiça Comum e também junto ao Conselho Regional de Classe a que pertencem estes Profissionais.
5	APROVAÇÃO EM CONDOMÍNIO: Os Responsáveis Técnicos ficam cientes que deverão cumprir as exigências impostas pelos mesmos e, quando necessário, aprovar o projeto nas Comissões de Obras ou Associações, não sendo necessária a sua apresentação junto à Prefeitura Municipal.
6	DIREITO DE VIZINHANÇA: Não haverá abertura de janelas, terraço ou varanda, com rebaixamento ao nível do terreno, pelo código civil. Serão atendidas todas as exigências definidas pelo Direito de Vizinhança.
7	ACESSIBILIDADE: Os Responsáveis Técnicos se obrigam, expressamente, quando aplicável, a edificação atenderá ao disposto nas legislações vigentes quanto à acessibilidade e NBR 9050/2015.
8	MOVIMENTO DE TERRA: Quando necessários os serviços de escavação e aterro, estes deverão atender as normas e especificações (escavação NBR 9061 e aterro NBR 5661 e NR 18) garantindo a estabilidade do solo e das edificações vizinhas e a segurança dos operários, bem como o atendimento à Lei Municipal 5980/2001.
9	LIMPEZA DO TERRENO: Ao serem retirados materiais orgânicos (mato) e entulho, deverão ser coletados por empresas especializadas e encaminhadas para áreas específicas destinadas para essa finalidade. A extração de solos, quando necessário, deverá ser executada mediante autorização da Secretaria do Meio Ambiente.
10	CANTEIRO DE OBRA: As instalações de canteiro (depósitos, processamento, tapume) deverão ocorrer exclusivamente dentro dos limites do lote. Quando utilizada parte da calçada deverá atender os artigos 24 e 25 da LC 2932/19.
11	SERVIÇOS GERAIS: Os projetos e a execução dos serviços de: Fundação, Superestrutura, Alvenaria e vedação, Forro, Cobertura, Revestimento de paredes e de pisos deverão atender à legislação vigente e normalização e específica, notadamente a NBR 15575/2013 Edificações Habitacionais - Desempenho; Parte 1-Requisitos Gerais; Parte 2-Sistemas Estruturais; Parte 3-Pisos, Parte 4-Vedação e Parte 5-Cobertura.
12	INSTALAÇÕES HIDRÁULICAS E SANITÁRIAS: O projeto e execução deverão atender: DECRETO 1820/18 - Regulamento de Serviços do DAERP; NBR 15575-6 Edificações Habitacionais - Desempenho; NBR 8160 Sistemas Prediais de Esgoto Sanitário - Projeto e Execução; NBR 5626 - Instalações Prediais de Água Fria; Normas específicas da ABNT. Quando a área de serviço for descoberta deverá ser previsto telhado sobre o tanque. Fica expressamente vedada a interconexão de Águas Pluviais no Sistema de Esgotos Sanitários e vice-versa.
13	INSTALAÇÕES ELÉTRICAS: Deverão ser projetadas e executadas de acordo com NBR 5410 e Normas da CPFL. Dotada de sistema de aterramento (condutor terra) conforme Lei Federal 11337/06.
14	ILUMINAÇÃO E VENTILAÇÃO: Os ambientes cujas condições de iluminação e ventilação são insuficientes serão suplementadas por meios mecânicos e artificiais, conforme LC 2932/19.
15	ÁREA PERMEÁVEL E CAIXA DE RETENÇÃO/INFILTRAÇÃO DE ÁGUAS PLUVIAIS: Atende ao disposto na LC 2932/19 (Código de Obras), LC 2157/07 (Lei de Uso do Solo) e demais legislações pertinentes e suas regulamentações.
16	CALÇADA E PASEIO PÚBLICO: Conforme Lei Municipal 19384/11 e NBR 9050/2015, o piso do passeio público será firme, antiderrapante, com inclinação transversal máxima de 3%. Todos os obstáculos, mobiliários urbanos e rebaixamentos de guia serão providos de piso tátil. O rebaixamento de guia atenderá o disposto na LC 2932/19. A calçada obedecerá a largura especificada no loteamento, em projeto urbanístico aprovado na P.U.P.
17	PLANTIO DE ÁRVORE: Conforme Lei Municipal 9437/11, ficam os proprietários obrigados a plantar e manter sob seus cuidados no mínimo 01 (uma) árvore defronte sua propriedade.
18	CAIXA DE CORRESPONDÊNCIA: Conforme Lei Municipal 132/82, deverá ser instalada caixa de correspondência com acesso externo ao alinhamento.
19	Todas as Leis e Normas mencionadas neste memorial deverão ser substituídas pelas alterações que lhes forem aplicadas ou Leis e Normas que venham substituí-las.

INSTRUÇÕES:

- Este arquivo padrão deverá ser utilizado para todos os tipos de processos, tanto físicos quanto eletrônicos;
- Para os projetos que necessitem de mais folhas, a primeira folha deverá conter a lista de declarações, podendo ser excluída nas demais folhas do processo.

PROCESSOS ELETRÔNICOS

Ver MANUAL DE INSTRUÇÕES que pode ser obtido através do endereço <http://www.ribeiraopreto.sp.gov.br/portal/planejamento/aprovacao-de-projetos>
A - Para inserção do carimbo ou legenda, siga as instruções do manual;
B - Atender padronização de desenho informada no manual.

PROCESSOS FÍSICOS

Ver MANUAL DE ORIENTAÇÃO PARA APRESENTAÇÃO DE PROJETOS DE EDIFICAÇÕES, que pode ser obtido através do endereço <http://www.ribeiraopreto.sp.gov.br/portal/planejamento/aprovacao-de-projetos>
A - Para inserção do carimbo ou legenda, siga as instruções do manual;
B - Atender padronização de desenho informada no manual.