




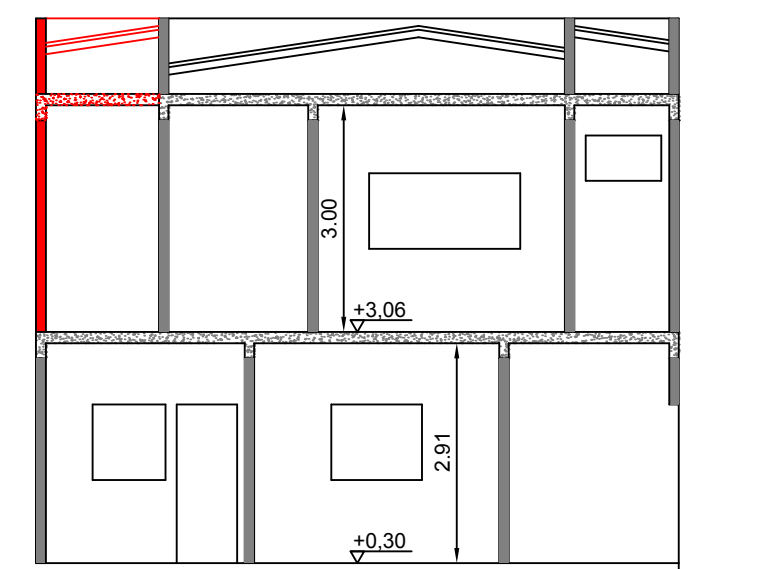

CORTE BB
escala 1:100

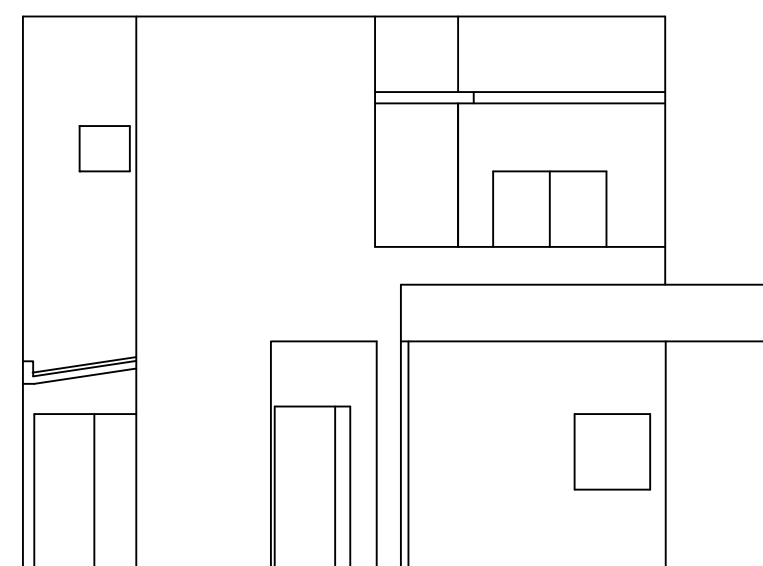


FACHADA
escala 1:100

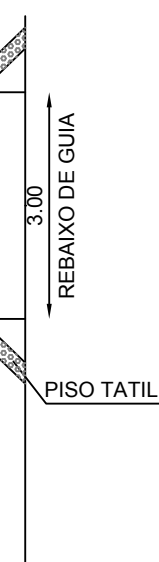


PROJETO
ARQUITETÔNICO
PADRÃO ANTERIOR
(RESIDENCIAL UNIFAMILIAR)


EXEMPLO MERAMENTE ILUSTRATIVO,
TODAS AS MEDIDAS E INFORMAÇÕES
DEVERÃO SER ADEQUADAS PARA A
SITUAÇÃO REAL DO PROJETO

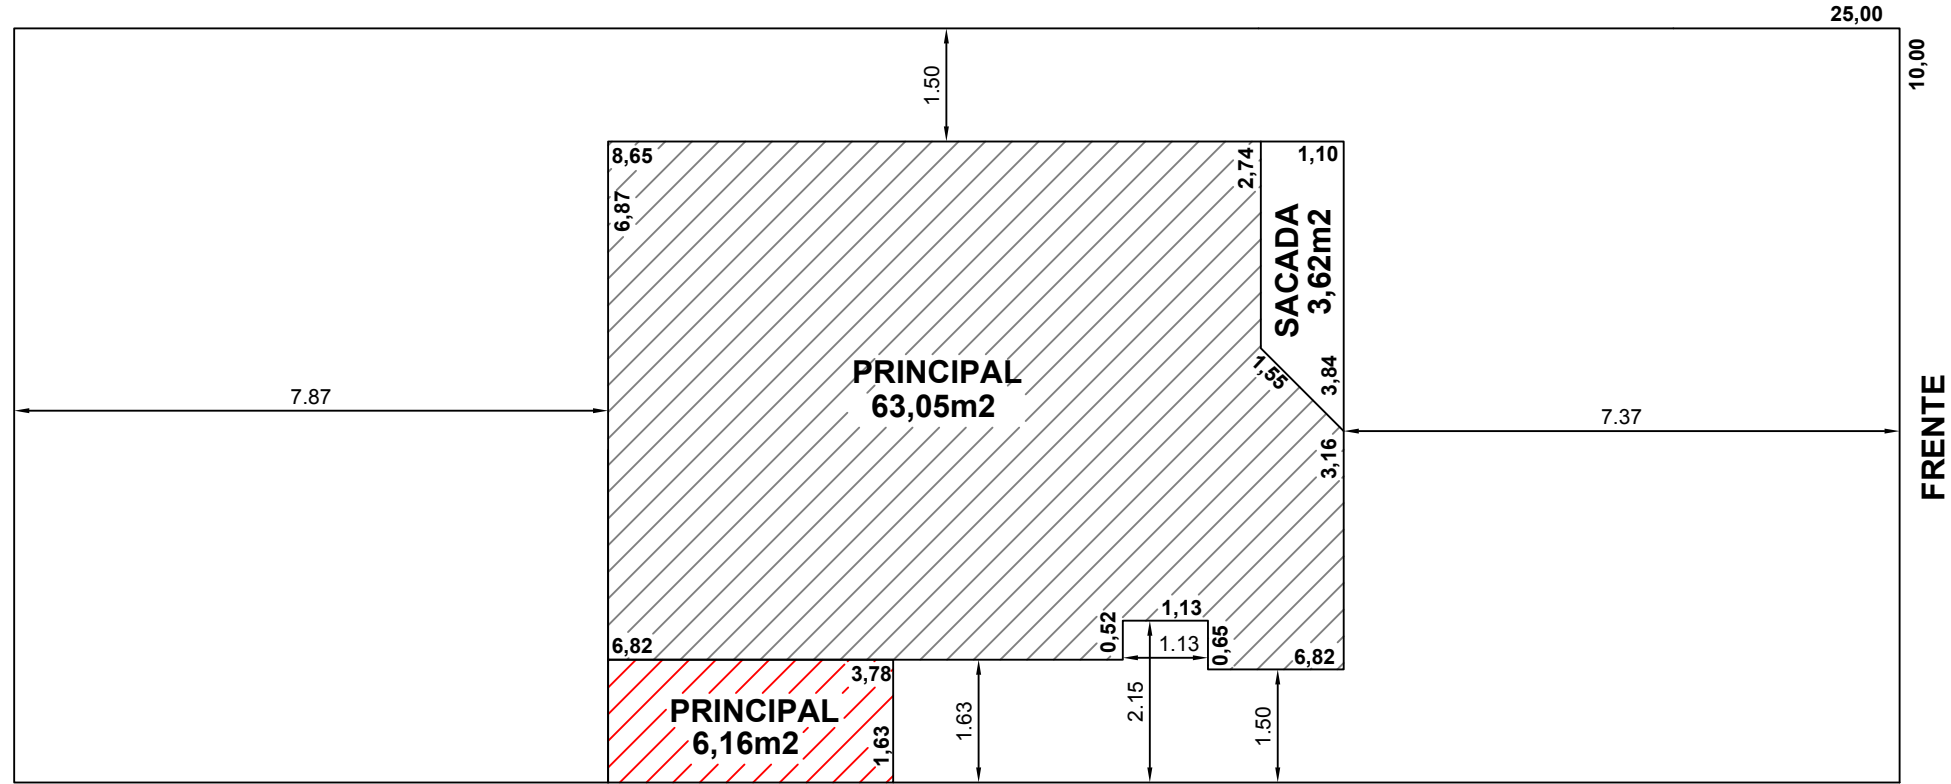

PLANTA PAV. SUPERIOR
escala 1:100

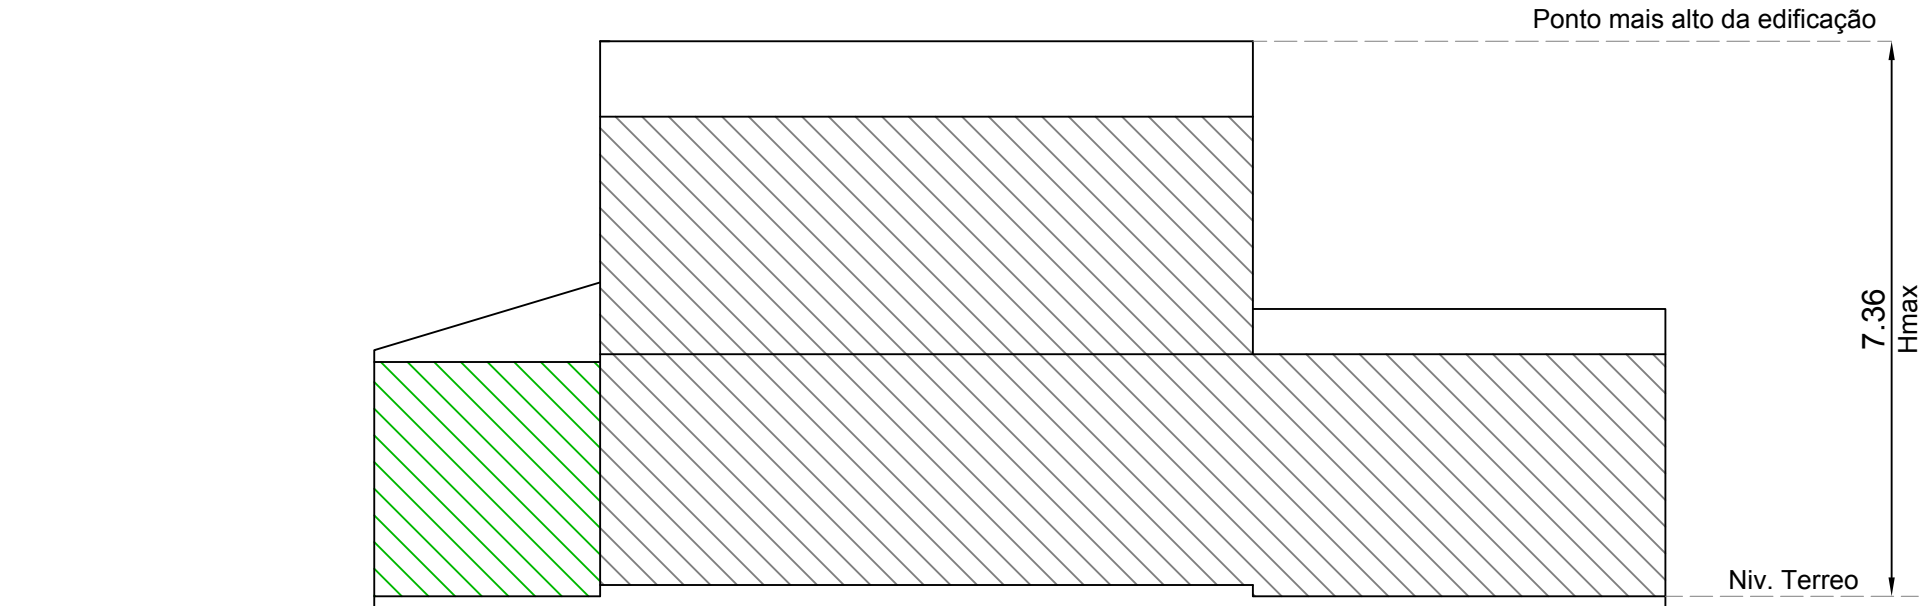

CORTE ESQUEMATICO
escala 1:100

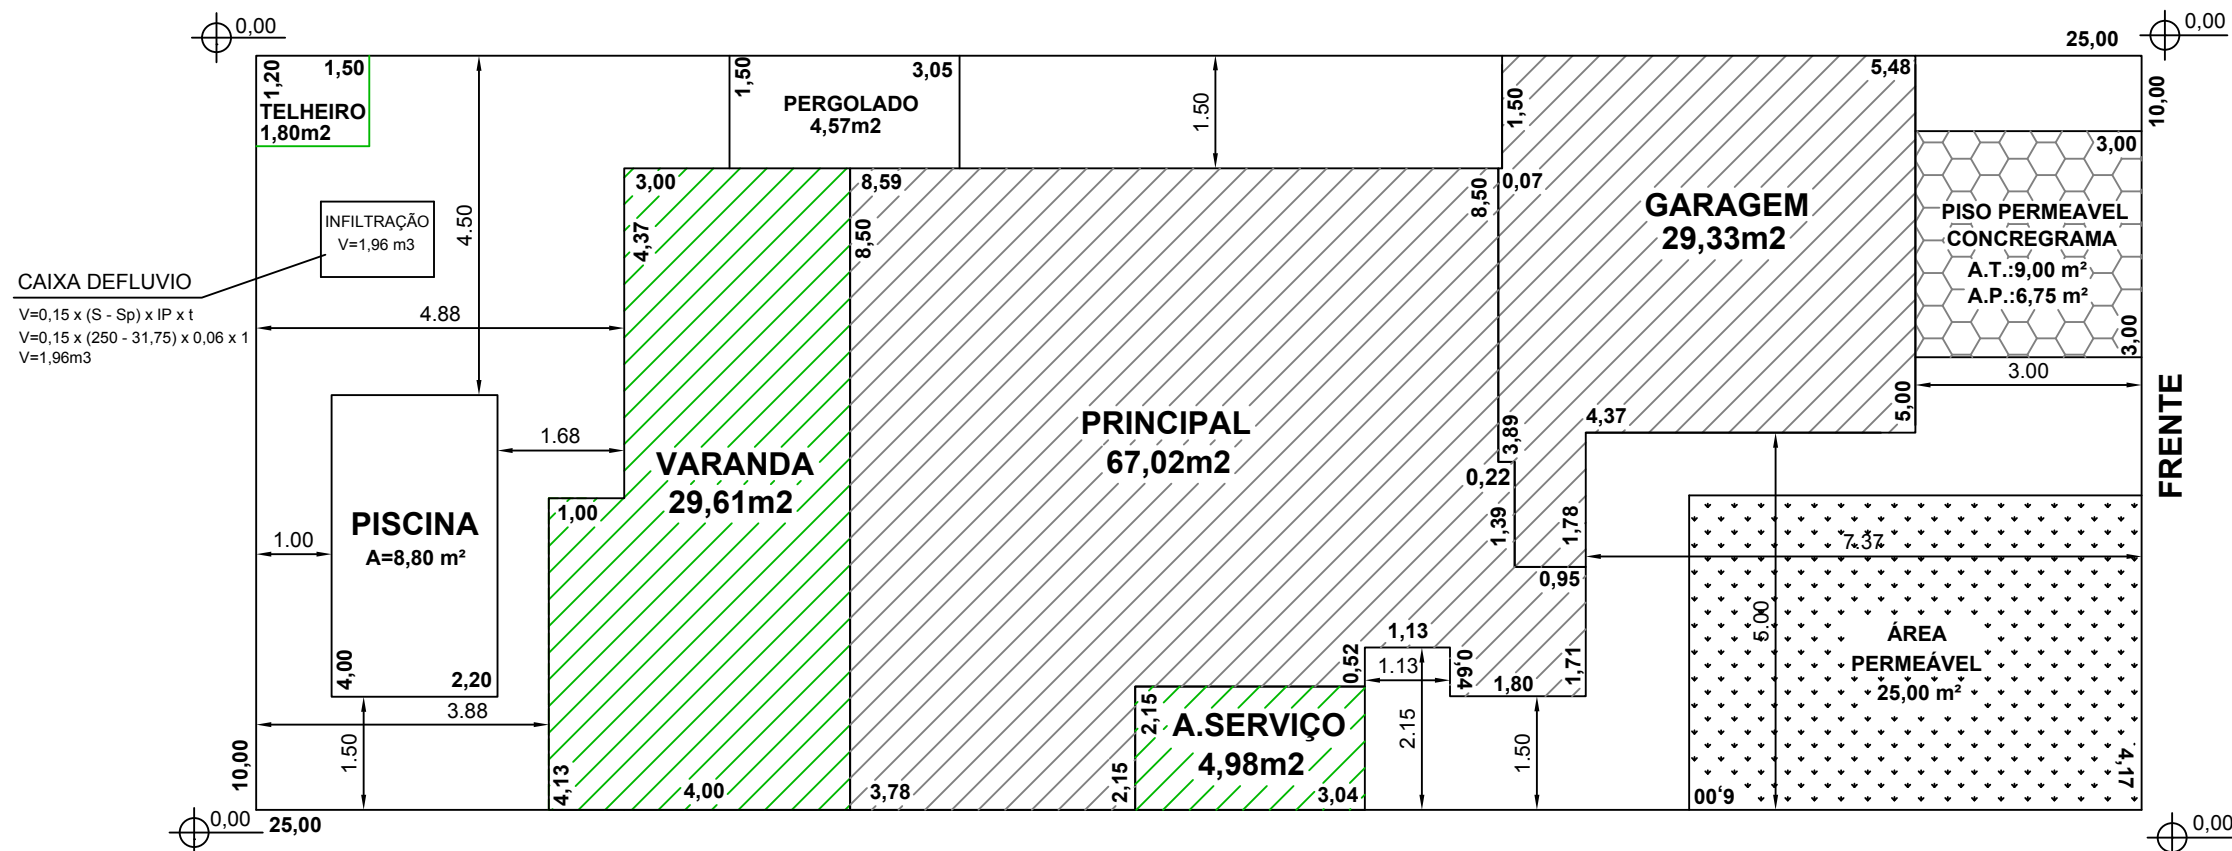

PLANTA PAV. TÉRREO
escala 1:100

LEGENDA

- ÁREA EXISTENTE
- ÁREA À REGULARIZAR
- ÁREA À CONSTRUIR
- ÁREA PERMEÁVEL - SOLO NATURAL
- PISO PERMEÁVEL
- OBRAS COMPLEMENTARES

DECLARAÇÕES - 2019	
1	LEGISLAÇÃO: Os responsáveis técnicos declaram ter pleno conhecimento da legislação municipal vigente, a saber, as Leis Complementares 2932 de 10 de Janeiro de 2019 (Código de Obras Municipal) e 2157/2007 (Lei de Parcelamento, Uso e Ocupação do Solo) e demais leis que regulamentam construções como o Decreto Estadual de Segurança Contra Incêndios das edificações e áreas de risco no Estado de São Paulo, as Leis e Decretos de Licenciamento ambientais, Plano de Proteção de Voo (CONAER), regulamentação da Vigilância Sanitária, Normas Regulamentadoras do Ministério do Trabalho, entre outros.
2	PROJETO SIMPLIFICADO e ANÁLISE SIMPLIFICADA: Com base na LC 2932/2019, Artigos 12 a 14, Decreto 028.019 - Institui e regulamenta Projeto Simplificado para aprovação de edificações residenciais e não residenciais e no Decreto 272/19 - Institui o procedimento de análise simplificada, aprovação de projeto e concessão de Alvará de Construção neste município, para edificações residenciais e não residenciais de todos os portes, tanto para procedimentos eletrônicos como físicos (impressos), serão realizadas análises simplificadas apenas sobre os itens especificados nas legislações e decretos citados. Todas as demais exigências legais e informações, além das here acima especificadas, constantes dos projetos apresentados, serão da exclusiva responsabilidade dos profissionais habilitados que, deram atendimento às legislações específicas, suas regulamentações, e das atribuições dos loteamentos/condomínios. Os responsáveis técnicos, na forma das leis a que estão submetidos, responderão pelas técnicas e formas de ocupação adotados no projeto.
3	REGULATIZAÇÃO OU LEGALIZAÇÃO: Quando se tratar de projeto de Regularização ou Legalização, havendo ou não reforma, reparo, intervenções estruturais, os responsáveis técnicos, declaram mediante a assinatura deste projeto que não foram encontradas irregularidades que comprometam a estrutura da obra e que o imóvel tem condições de habitabilidade, não oferecendo qualquer tipo de risco aos seus usuários.
4	DIVERGÊNCIAS ENTRE PROPRIETÁRIO E RESPONSÁVEIS TÉCNICOS: Quaisquer divergências entre os Responsáveis Técnicos pela Elaboração do Projeto, pela Execução da Obra e Proprietário, deverão ser tratadas e eliminadas no âmbito da Justiça Comum e também junto ao Conselho Regional de Classe a que pertencem estes Profissionais.
5	APROVAÇÃO EM CONDOMÍNIO: Os Responsáveis Técnicos ficam cientes que deverão cumprir as exigências impostas pelos mesmos e, quando necessário, a provar o projeto nas Comissões de Obras ou Associações, não sendo necessária a sua apresentação junto à Prefeitura Municipal.
6	DIREITO DE VIZINHANÇA: Não haverá abertura de janelas, terraço ou varanda, com recuos inferiores ao estabelecido pelo código civil. Serão atendidas todas as exigências definidas pelo Direito de Vizinhança.
7	ACESSIBILIDADE: Os Responsáveis Técnicos declaram, expressamente, quando aplicável, a edificação atender à disposição nas legislações vigentes quanto à acessibilidade e NBR 9062/2015.
8	MOVIMENTO DE TERRA: Quando necessários os serviços de escavação e aterro, estes deverão atender as normas específicas (escavação NBR 9061 e NBR 5618) garantindo a estabilidade do solo e das edificações vizinhas e a segurança dos operários, bem como o atendimento à Lei Municipal 15930/2001.
9	LIMPEZA DO TERRENO: Ao serem retirados materiais orgânicos (mato) e entulho, deverão ser coletados por empresas especializadas e encaminhadas para áreas específicas destinadas para essa finalidade. A extração de árvores, quando necessário, deverá ser executada mediante autorização da Secretaria do Meio Ambiente.
10	CANTEIRO DE OBRAS: As instalações de canteiro (depósitos, processamento, limpeza) deverão ocorrer exclusivamente dentro dos limites do lote. Quando utilizada parte da calçada deverá atender os artigos 24 e 25 da LC 2932/19.
11	SERVIÇOS GERAIS: Os projetos e a execução dos serviços de: Fundação, Superestrutura, Alvenaria e vedação, Forro, Cobertura, Revestimento de paredes e de pisos deverão atender à legislação vigente e no município específica, notadamente a NBR 15575/2013 Edificações Habitacionais — Desempenho; Parte 1-Requisitos Gerais; Parte 2-Sistemas Estruturais; Parte 3-Pisos; Parte 4-Vedações e Parte 5-Coberturas.
12	INSTALAÇÕES HIDRÁULICAS E SANITÁRIAS: O projeto e a execução deverão atender: DECRETO 18/2018 - Regulamento de Serviços do DAE-PP; NBR 15575-6 Edificações - Habitação - De desempenho; NBR 6160 Sistema Prediais de Esgoto Sanitário - Projeto e Execução; NBR 5626 - Instalações Prediais de Água Fria; Normas específicas da ABNT Quando a área de serviço for descoberta deve ser previsto telhado sobre o tanque. Fica expressamente VEDADA a Interconexão de Águas Pluviais no Sistema de Esgotos Sanitários e vice-versa.
13	INSTALAÇÕES ELÉTRICAS: Deverão ser projetadas e executadas de acordo com NBR 5410 e Normas da CPTI. Dotada de sistema de aterramento (conduto terra) conforme Lei Federal 11337/06.
14	ILUMINAÇÃO E VENTILAÇÃO: Os ambientes cujas condições de iluminação e ventilação são insuficientes serão suplementadas por meios mecânicos e artificiais, conforme LC 2932/19.
15	ÁREA PERMEÁVEL E CAIXA DE RETENÇÃO/INFILTRAÇÃO DE ÁGUAS PLUVIAIS: Atende à disposto na LC 2932/19 (Código de Obras), LC 2157/07 (Lei de Uso de Parcelamento do Solo), outras legislações pertinentes e suas regulamentações.
16	CALÇADA E PASSARELO PÚBLICO: Conforme Lei Municipal 3384/11 e NBR 9060/2015, o piso do passeio público será firme, antiderrapante, com inclinação transversal máxima de 3%. Todos os obstáculos, mobiliários urbanos e equipamentos de guia serão providos de piso tátil. O rebaixamento de guia atenderá o disposto na LC 2932/19. A calçada obedecerá a largura estabelecida no loteamento, em projeto urbanístico aprovado no P.M.P.P.
17	PLANTIO DE ÁRVORES: Conforme Lei Municipal 9437/11, ficam os proprietários obrigados a plantar e manter sob seus cuidados no mínimo 01 (uma) árvore de frente sua propriedade.
18	CAIXA DE CORRESPONDÊNCIA: Conforme Lei Municipal 132/92, deverá ser instalada caixa de correspondência com acesso externo ao alinhamento.
19	Todas as Leis e Normas relacionadas neste memorial deverão ser substituídas pelas alterações que lhes forem aplicadas ou Leis e Normas que venham substituí-las.

EXEMPLO MERAMENTE ILUSTRATIVO,
TODAS AS MEDIDAS E INFORMAÇÕES
DEVERÃO SER ADEQUADAS PARA A
SITUAÇÃO REAL DO PROJETO