



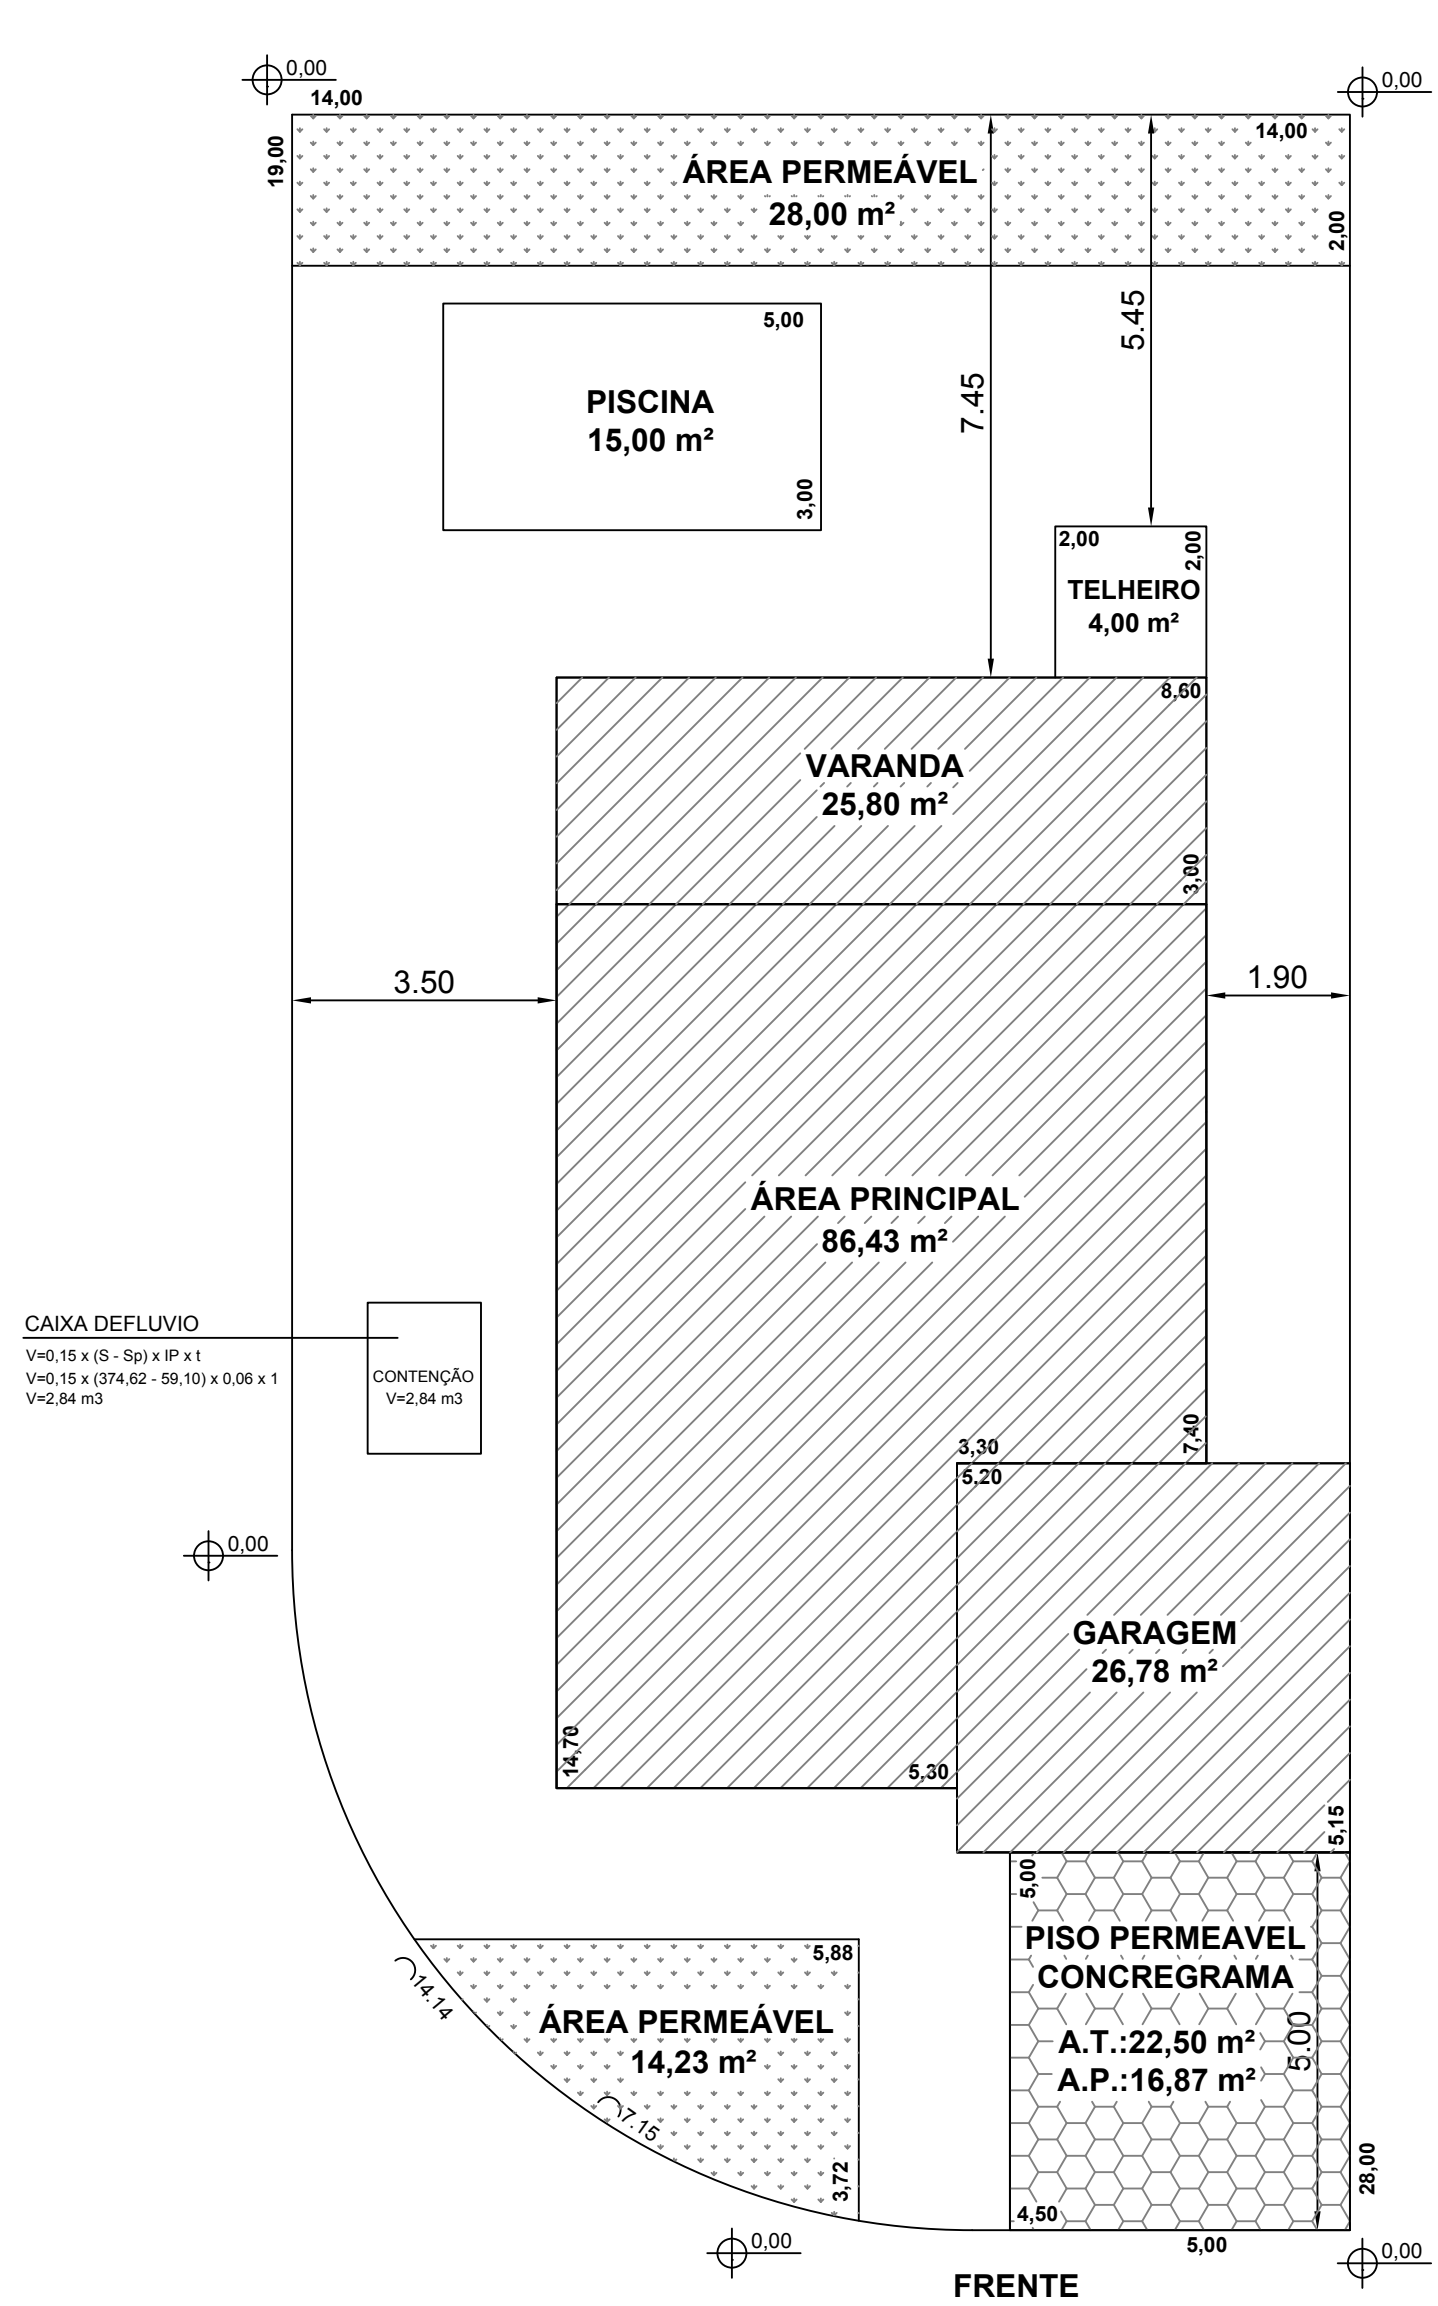

PAV. TERREO
Escala 1:100

CORTE ESQUEMATICO
Escala 1:100

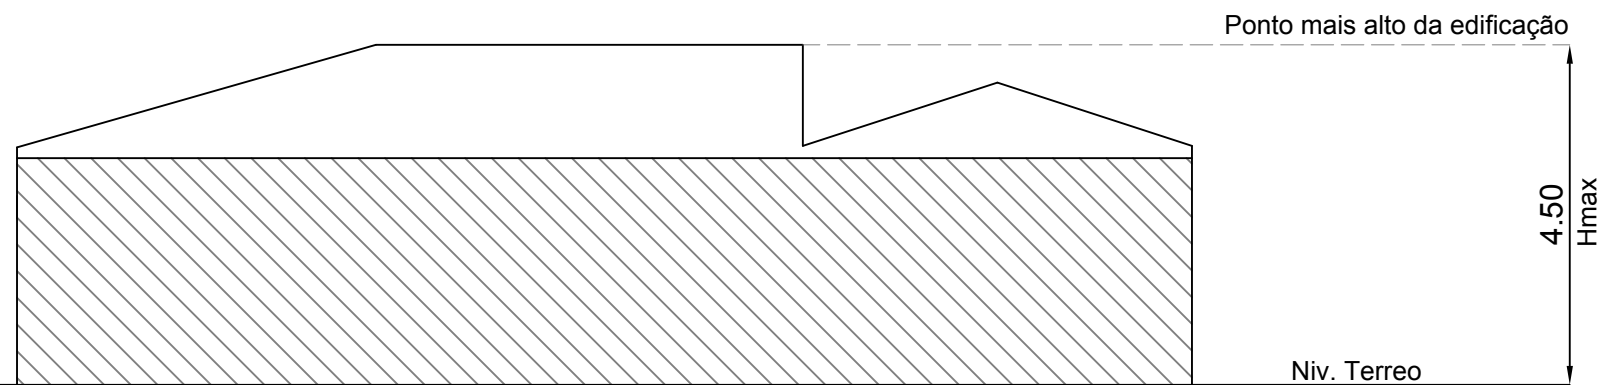

DECLARAÇÕES - 2019	
1	LEGISLAÇÃO: Os responsáveis técnicos declaram ter pleno conhecimento da legislação municipal vigente, a saber, as Leis Complementares 2932 de 10 de Janeiro de 2019 (Código de Obras Municipais) e 2157/2007 (Lei de Parcelamento, Uso e Ocupação do Solo) e demais leis que regulamentam construções como o Decreto Estadual de Segurança Contra Incêndios das edificações e as leis de risco no Estado de São Paulo, as Leis e Decretos de licenciamento ambiental, Plano de Proteção de Voo (COMAER), regulamentação da Vigilância Sanitária, Normas Regulamentadoras do Ministério do Trabalho, entre outros.
2	PROJETO SIMPLIFICADO e ANÁLISE SIMPLIFICADA: Com base na LC 2932/2019, Artigos 12 a 14, Decreto 028/2019 - Institui e regulamenta Projeto Simplificado para aprovação de edificações residenciais e não residenciais e no Decreto 272/19 - Institui o procedimento de análise simplificada, aprovação de projeto e concessão de Alvará de Construção neste município, para edificações residenciais e não residenciais de todos os portes, tanto para procedimentos eletrônicos como físicos (impressos), serão realizadas análises simplificadas apenas sobre os itens especificados nas legislações e decreto citado. Todas as demais exigências legais e informações, além dos itens acima especificados, constantes dos projetos apresentados, serão de exclusiva responsabilidade dos profissionais habilitados que, declaram atendimentos das legislações específicas, suas regulamentações, e das restrições dos loteamentos/condomínios. Os responsáveis técnicos, na forma das leis a que estão submetidos, responderão pelas técnicas e formas de ocupação adotadas no projeto.
3	REGULARIZAÇÃO OU LEGALIZAÇÃO: Quando se tratar de projeto de Regularização ou Legalização, havendo ou não reforma, reparo, intervenções estruturais, os responsáveis técnicos, declaram mediante a assinatura deste projeto que não foram encontradas irregularidades que comprometam a estrutura da obra e que o imóvel tem condições de habitabilidade, não oferecendo qualquer tipo de risco aos seus usuários.
4	DIVERGÊNCIAS ENTRE PROPRIETÁRIO E RESPONSÁVEIS TÉCNICOS: Quaisquer divergências entre os Responsáveis Técnicos pela Elaboração do Projeto, pela Execução da Obra e Proprietário, deverão ser tratadas e eliminadas no âmbito da Justiça Comum e também junto ao Conselho Regional de Classe a que pertencem estes Profissionais.
5	APROVAÇÃO EM CONDOMÍNIO: Os Responsáveis Técnicos ficam cientes que deverão cumprir as exigências impostas pelos mesmos e, quando necessário, aprovar o projeto nas Comissões de Obras ou Associação, não sendo necessária a sua apresentação junto à Prefeitura Municipal.
6	DIREITO DE VIZINHANÇA: Não haverá abertura de janelas, terraço ou varanda, com recuo inferior ao estabelecido pelo código civil. Serão atendidas todas as exigências definidas pelo Direito de Vizinhança.
7	ACESSIBILIDADE: Os Responsáveis Técnicos declaram, expressamente, quando aplicável a edificação atenderá ao disposto nas legislações vigentes quanto à acessibilidade e NBR 9060/2015.
8	MOVIMENTO DE TERRA: Quando necessários os serviços de escavação e aterro, estes deverão atender as normas específicas (escavação NBR 9061 e aterro NBR 5681 e NBR 118) garantindo a estabilidade do solo e das edificações vizinhas e a segurança dos operários, bem como o atendimento à Lei Municipal 5902/2001.
9	LIMPEZA DO TERRENO: Ao serem retirados materiais orgânicos (mato) e entulho, deverão ser coletados e por empresas especializadas e encaminhadas para áreas específicas destinadas para essa finalidade. A extração de árvores, quando necessário, deverá ser executada mediante autorização da Secretaria do Meio Ambiente.
10	CANTEIRO DE OBRAS: As instalações de canteiro (depósitos, processamento, tapume) deverão ocorrer exclusivamente dentro dos limites do lote. Quando utilizada parte da calçada deverá atender os artigos 24 e 25 da LC 2932/19.
11	SERVIÇOS GERAIS: Os projetos e a execução dos serviços de: Fundação, Superestrutura, Alvenaria e vedação, Pórtico, Cobertura, Revestimento de paredes e de piso deverão atender a legislação vigente e normatização específica, notadamente a NBR 15575/2013 Edificações Habitacionais — Desempenho, Parte 1-Requisitos Gerais, Parte 2-Sistemas Estruturais, Parte 3-Pisos, Parte 4-Vedação e Parte 5-Cobertura.
12	INSTALAÇÕES HIDRÁULICAS E SANITÁRIAS: O projeto e a execução deverão atender: DECRETO 18/2018 - Regulamento de Serviços do DAERP, NBR 15575-6 Edificações Habitacionais - Desempenho, NBR 8160 Sistemas Prediais de Esgoto Sanitário - Projeto e Execução, NBR 5626 - Instalações Prediais de Água Fria, Normas específicas do ABNT. Quando a área de serviço for descoberta deverá ser previsto telhado sobre o tanque. Fica expressamente VEDADA a interconexão de Águas Pluviais no Sistema de Esgotos Sanitários e vice-versa.
13	INSTALAÇÕES ELÉTRICAS: Deverão ser projetadas e executadas de acordo com NBR 5410 e Normas da CPFL. Dotada de sistema de aterramento (condutor terra) conforme Lei Federal 11133/06.
14	ILUMINAÇÃO E VENTILAÇÃO: Os ambientes cujas condições de iluminação e ventilação são insuficientes serão suplementadas por meios mecânicos e artificiais, conforme LC 2932/19.
15	ÁREA PERMEÁVEL E CAIXA DE RETENÇÃO/INFILTRAÇÃO DE ÁGUAS PLUVIAIS: Atenderá disposto na LC 2932/19 (Código de Obras), LC 2157/07 (Lei de Uso e de Parcelamento do Solo), outras legislações pertinentes e suas regulamentações.
16	CALÇADA E PASEIO PÚBLICO: Conforme Lei Municipais 3840/11 e NBR 9058/2015, o piso do passeio público será firme, antiderrapante, com inclinação transversal máxima de 3%. Todos os obstáculos, mobiliários urbanos e equipamentos de guia serão providos de piso tátil. O rebaixamento de guia atenderá o disposto na LC 2932/19. A calçada obedecerá a largura especificada no loteamento, em projeto urbanístico aprovado na PMPP.
17	PLANTIO DE ÁRVORE: Conforme Lei Municipal 9437/11, ficam os proprietários obrigados a plantar e manter sob seus cuidados no mínimo 01 (uma) árvore defronte sua propriedade.
18	CAIXA DE CORRESPONDÊNCIA: Conforme Lei Municipal 132/92, deverá ser instalada caixa de correspondência com acesso externo ao alinhamento.
19	Todas as Leis e Normas relacionadas neste memorial deverão ser substituídas pelas alterações que lhes forem aplicadas ou Leis e Normas que venham substituí-las.

LEGENDA

CONSTRUÇÕES

- ÁREA EXISTENTE
- ÁREA A REGULARIZAR/LEGALIZAR
- ÁREA A CONSTRUIR/CONSTRUÇÃO
- ÁREA A DEMOLIR
- OBRAS COMPLEMENTARES

ÁREAS PERMEÁVEIS

- ÁREA PERMEÁVEL - SOLO NATURAL
- PISO PERMEÁVEL

NOVO PROJETO SIMPLIFICADO (RESIDENCIAL UNIFAMILIAR)

INSERIR CARIMBO GERADO ELETRONICAMENTE

QUADRO DE ÁREAS

TERRENO.....374,62m2

A CONSTRUIR

PRINCIPAL.....86,43m2

GARAGEM.....26,78m2

VARANDA.....25,80m2

TOTAL CONSTRUIR.....139,01m2

PISCINA.....15,00m2

TOTAL GERAL.....154,01m2

TAXA OCUPAÇÃO.....37,11%

A. PERMEÁVEL (15,78%)...59,10m2

EXEMPLO MERAMENTE ILUSTRATIVO, TODAS AS MEDIDAS E INFORMAÇÕES DEVERÃO SER ADEQUADAS PARA A SITUAÇÃO REAL DO PROJETO